



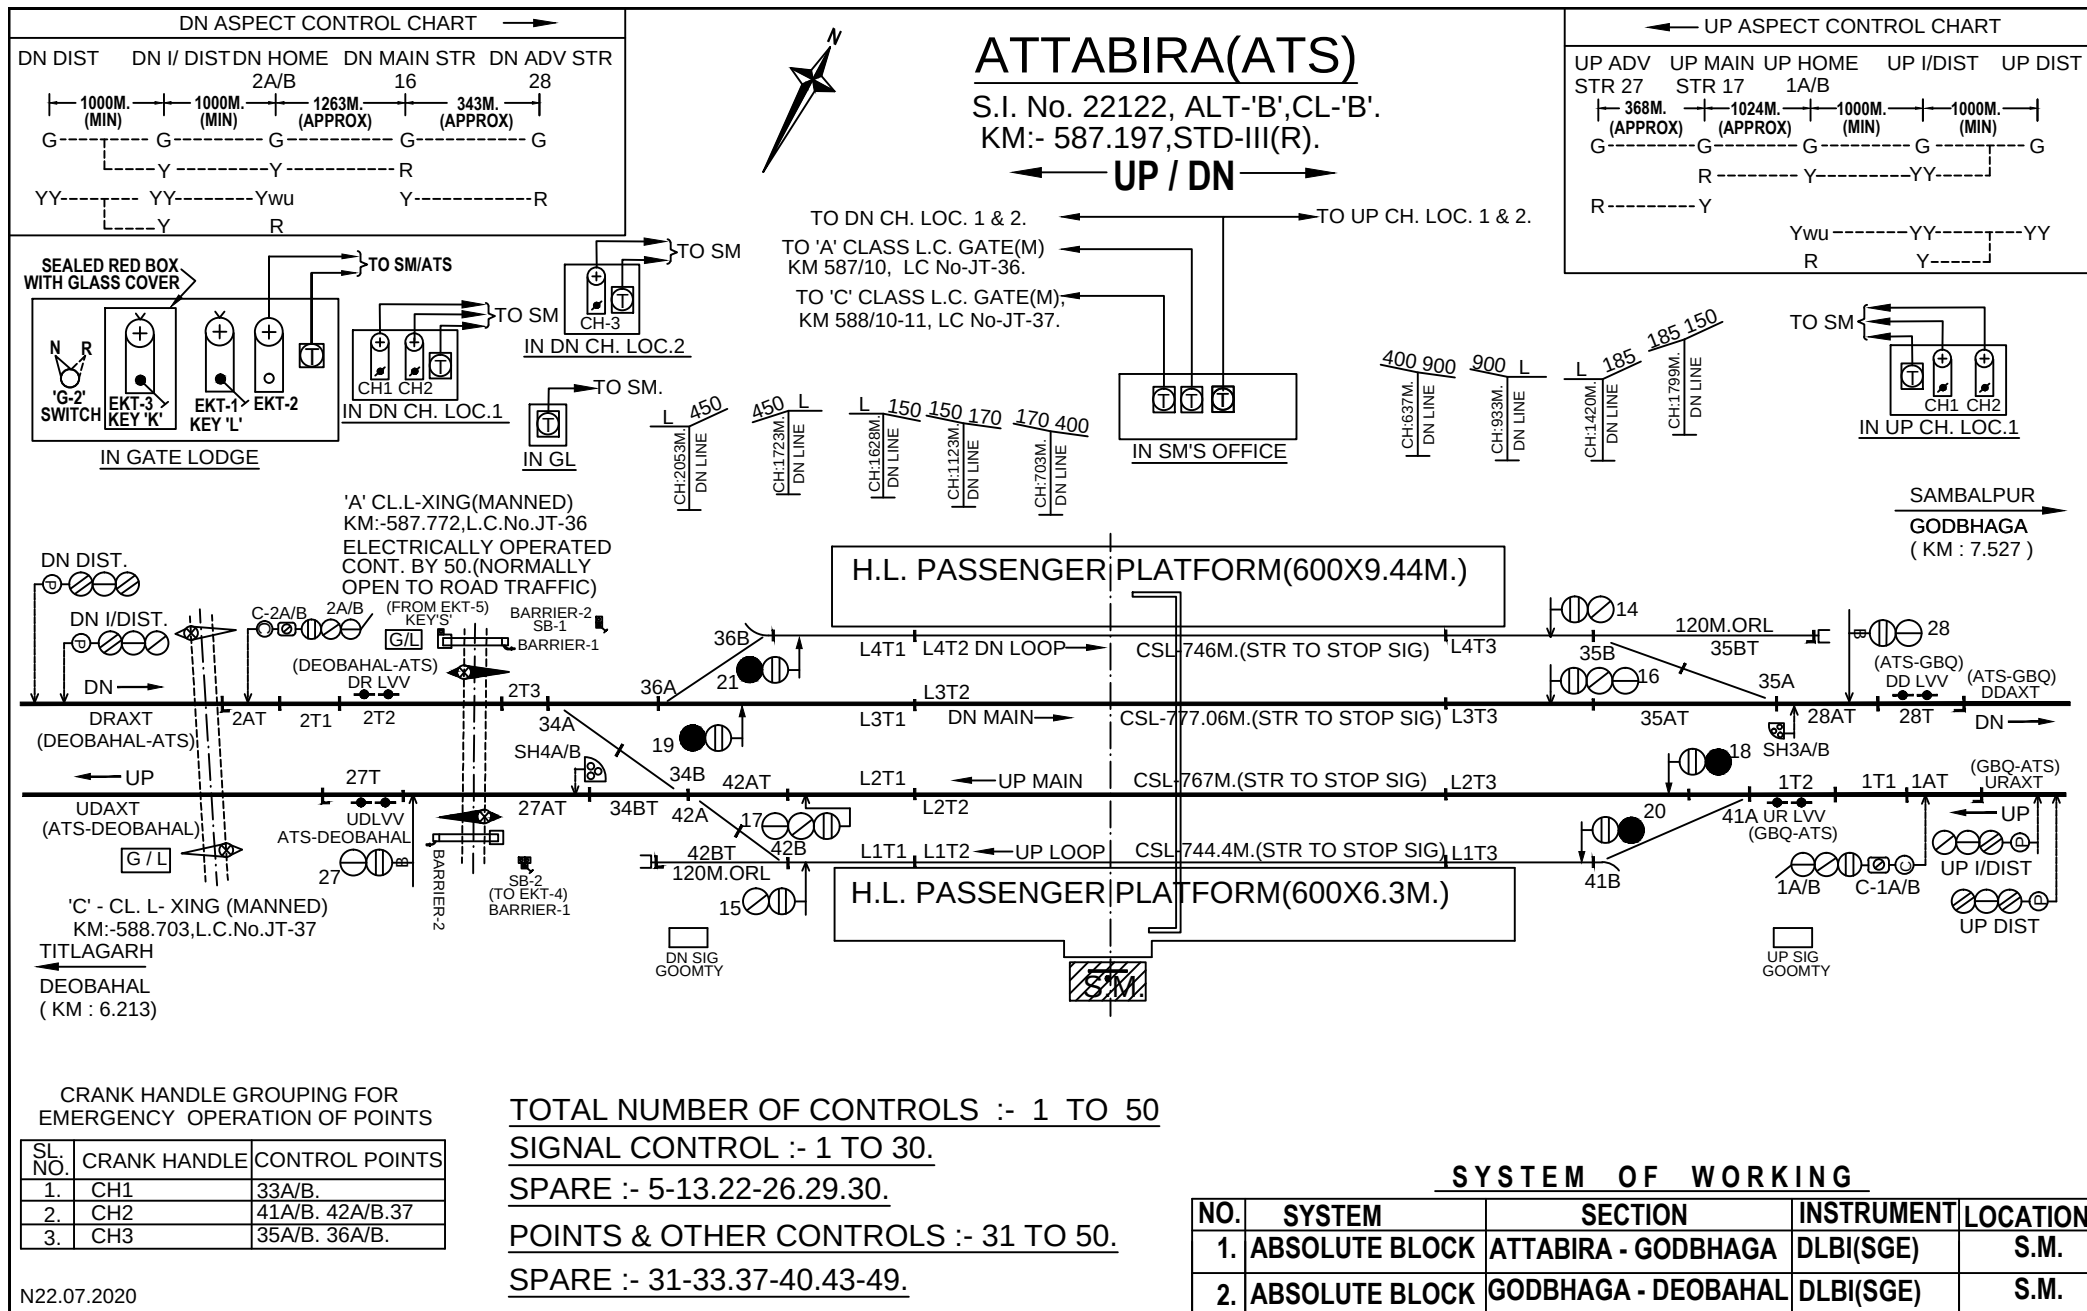

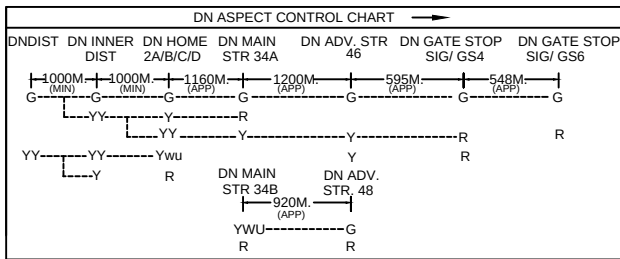

BALANGIR(BLGR)



S.I. No. - 22202, (E.I)
KM:- 681.004 F/HWH
STD-I (R), PH-II, CL-'B'.

UP / DN

TO DN CH. LOC- 1,2,3,4
TO UP IB POST LOC.
AT KM:690.494
TO 'C'.CL.L-XING(M),LC NO:JT-99
KM:682/33-35(UP),KM:682/34-36(DN)
TO 'A'.CL.L-XING(M),LC NO:JT-98
KM:681/11, KM:681/32-36(DN)



TO UP CH. LOC-1, 2,3,4,5,6 & 7.
TO 'C'.CL.L-XING (M),LC NO:JT-96
AT KM:679/3-5(UP),KM:679/4-6(DN)
TO 'A'.CL.L-XING(M),LC NO:JT-95
AT KM:678/21-23(UP),KM:678/22-24(DN)
TO 'C'.CL.L-XING (M),LC NO:JT-94
AT KM:678/11-13(UP),KM:678/12-14(DN)
TO DN IB POST LOC.
AT KM:670.845

IN SM'S OFFICE

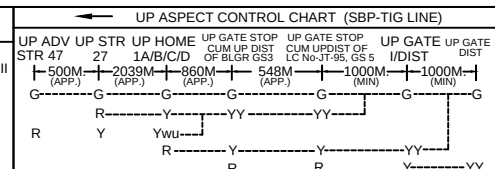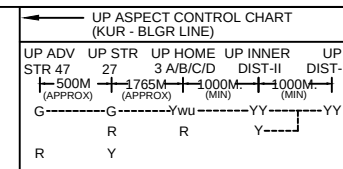


CRANK HANDLE GROUPING FOR EMERGENCY OPERATION OF POINTS

SL. NO.	CRANK HANDLE	CONTROL POINTS
1.	CH1	51A/B.
2.	CH2	53
3.	CH3	55A/B, 59A/B, 60A/B, 73A/B.
4.	CH4	57A/B, 58A/B.
5.	CH5	67A/B, 77A/B.
6.	CH6	56A/B, 81A/B.
7.	CH7	69
8.	CH8	79
9.	CH9	61A/B, 63A/B, 65, 71.
10.	CH10	75A/B.
11.	CH11	62, 64A/B.
12.	CH12	52A/B, 54A/B.

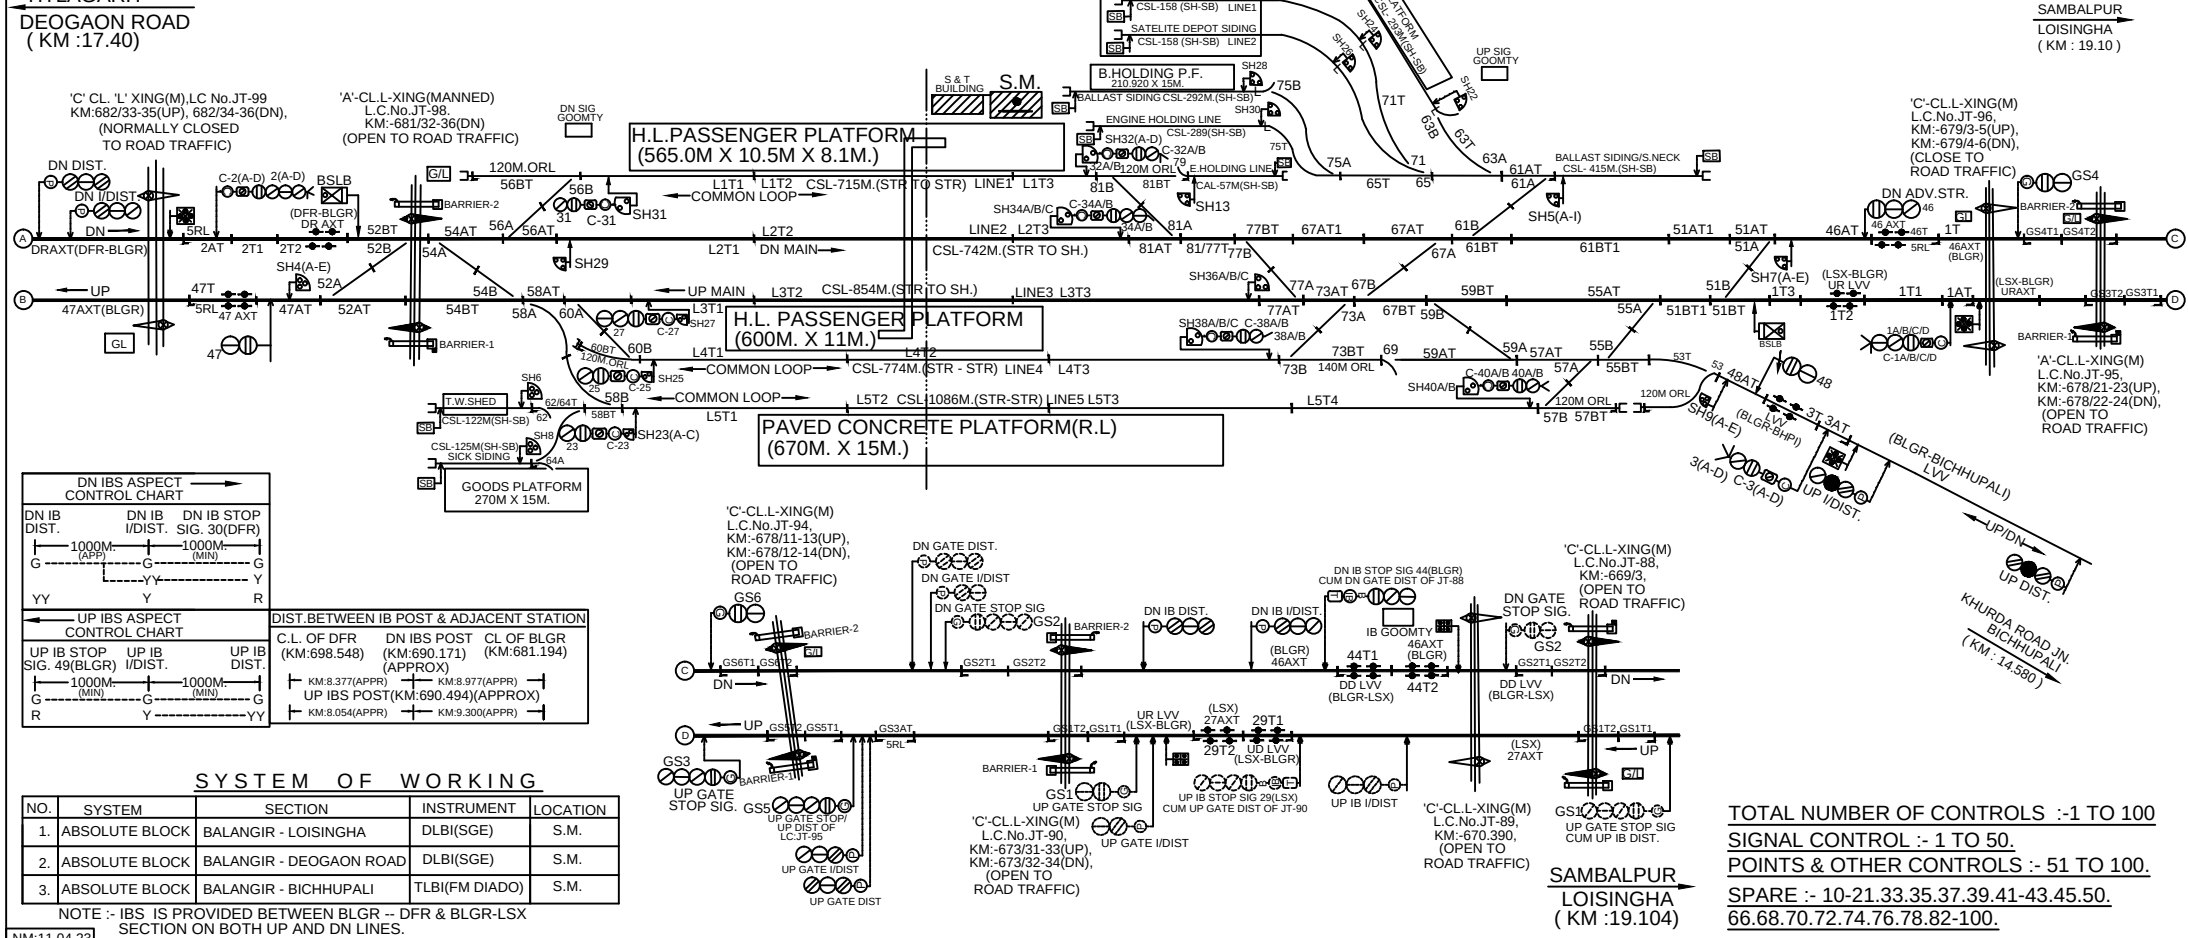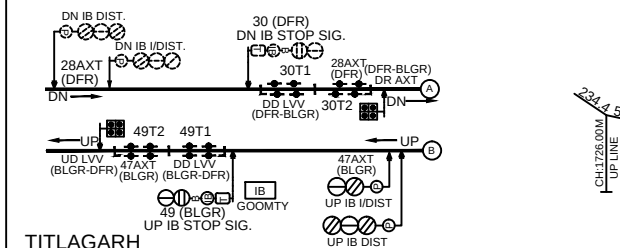

DN ASPECT CONTROL CHART


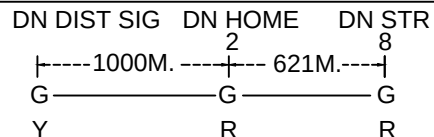


BPSL BLOCK CABIN

S.I. NO. 22124 ALT-'C', (P.I)
KM:524.327F/HWH, STD- II(R), CL-'SPL'
CH:5127F/LPG, CH:3669 F/BXQ
KM:524/10-8(DN), KM:524/7-9(UP)

UP / DN

UP ASPECT CONTROL CHART

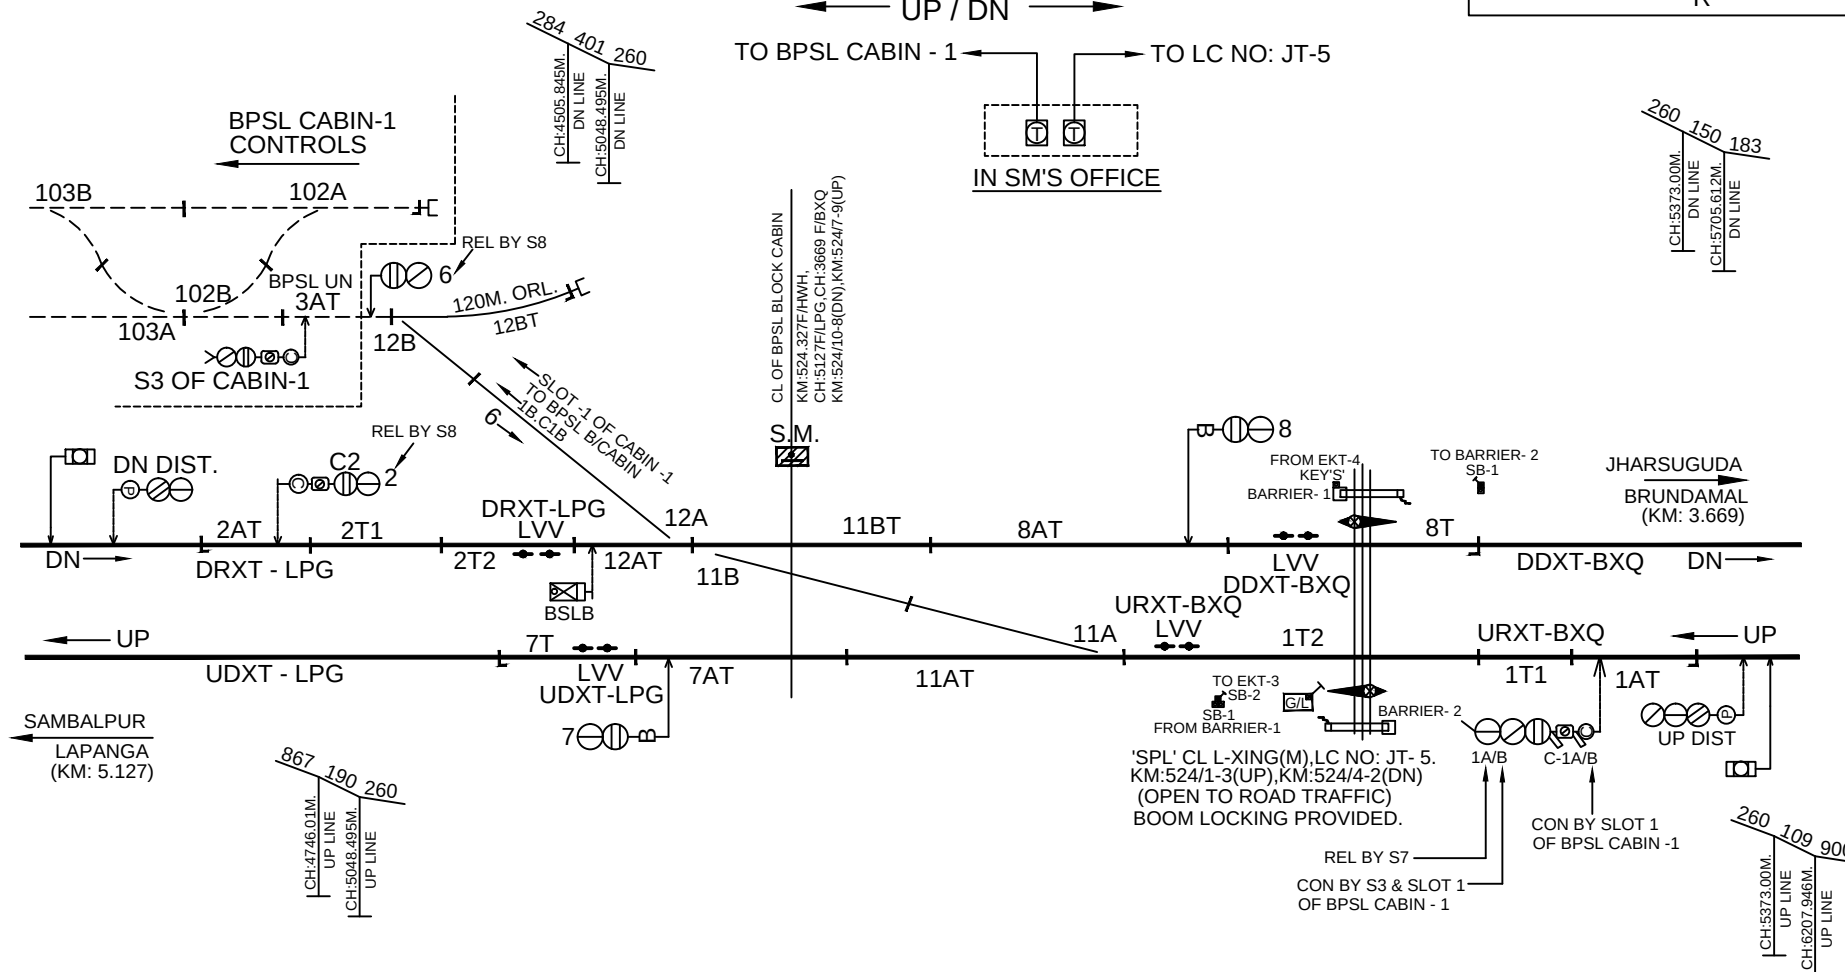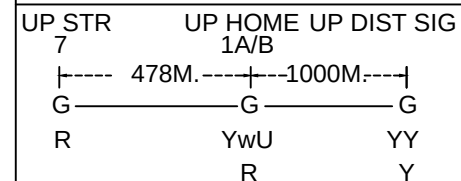

CRANK HANDLE GROUPING FOR EMERGENCY OPERATION OF POINTS

SL. NO.	CRANK HANDLE	CONTROL POINTS	AVAILABLE AT
1.	CH1	11A/B.	SM ROOM
2.	CH2	12A/B.	SM ROOM

CONTROL PANEL IN S.M.

TOTAL NUMBER OF CONTROLS :- 1 TO 20
SIGNAL CONTROLS :- 1. 2. 6. 7. 8.
POINTS & OTHER CONTROLS :- 11. 12. 19.
SPARE :- 3.4.5.9.10.13.14.15.16.17.18.20.





SYSTEM OF WORKING

No.	SYSTEM	SECTION	INSTRUMENT	LOCATION
1.	ABSOLUTE BLOCK	BPSL BLOCK CABIN - LPG	DLBI	SM's ROOM
2.	ABSOLUTE BLOCK	BPSL BLOCK CABIN - BXQ	DLBI	SM's ROOM
3.	INTER SLOTING	BPSL B.CABIN - BPSL CABIN-1	----	SM's ROOM




S.I. No.- 22215, (E.I),STD-III(R),
KM:- 605.377 F/HWH,CL-'SPL'.

← UP / DN →

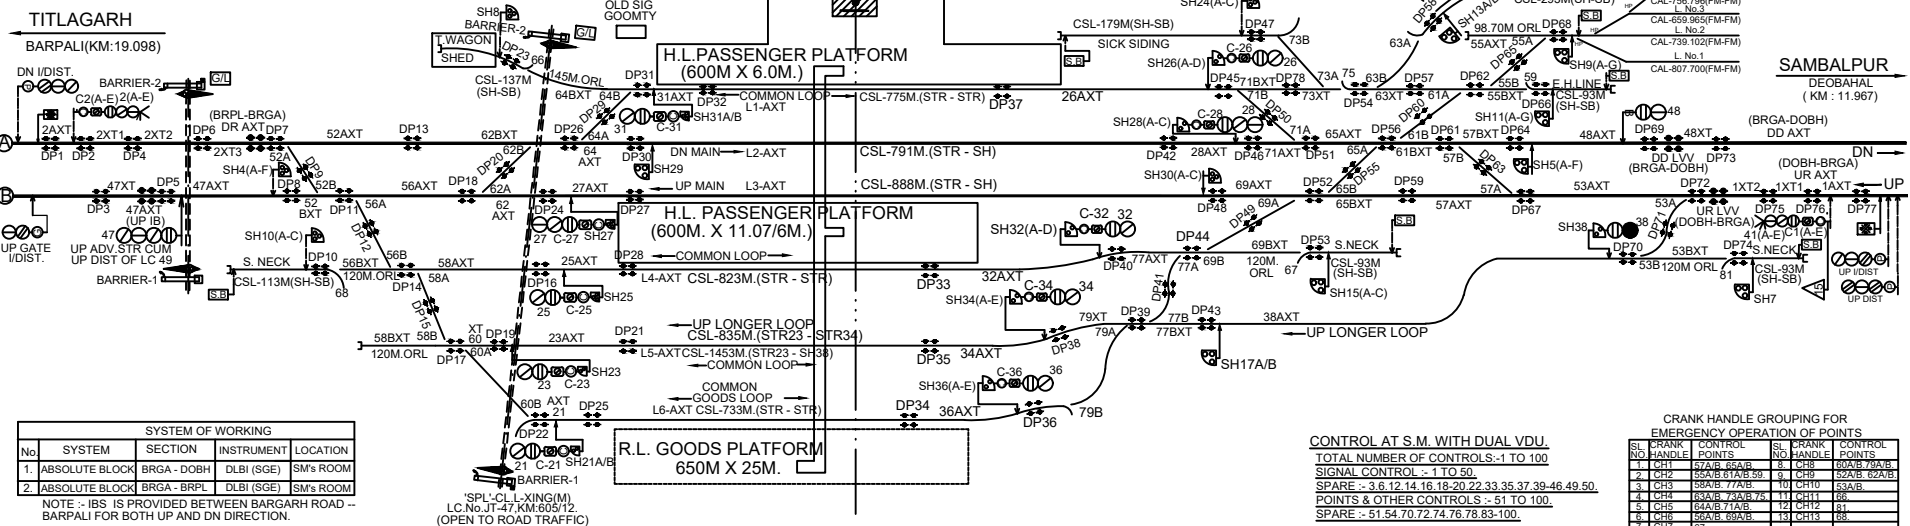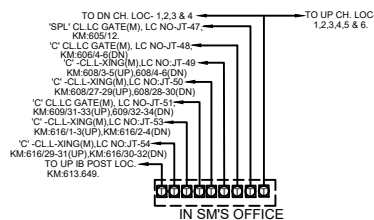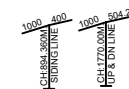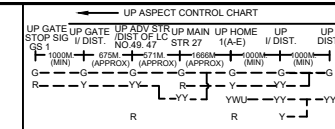


SL NO	CRANK HANDLE	CONTROL POINTS	SL NO	CRANK HANDLE	CONTROL POINTS
1	CH1	57A/B, 65A/B	8	CH8	80A/B, 79A/B
2	CH2	55A/B, 81A/B, 59	9	CH9	52A/B, 62A/B
3	CH3	58A/B, 77A/B	10	CH10	53A/B
4	CH4	63A/B, 73A/B, 75	11	CH11	86
5	CH5	64A/B, 71A/B	12	CH12	81
6	CH6	56A/B, 69A/B	13	CH13	88
7	CH7	67			

CONTROL AT S.M. WITH DUAL VDU.
TOTAL NUMBER OF CONTROLS:-1 TO 100
SIGNAL CONTROL :- 1 TO 50.
 SPARE :- 3.6.12.14.16.18-20.22.33.35.37.39-46.49.50.
POINTS & OTHER CONTROLS :- 51 TO 100.
 SPARE :- 51.54.70.72.74.76.78.83-100.

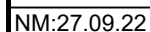

DN ASPECT CONTROL CHART

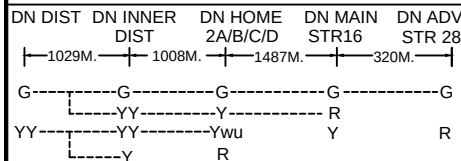


BADMAL(BUDM)

S.I. No.- 22217 (PH-II),(E.I),CL-'B'.
KM:- 724.665 F/HWH,STD-III(R)

UP / DN

UP ASPECT CONTROL CHART

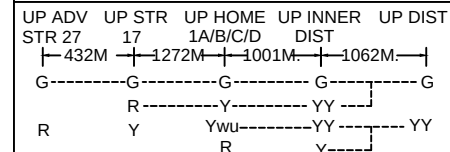


TO DN CH. LOC- 1,2,3 & 4. TO UP CH. LOC-1,2,3 & 4.



PASSENGER P.F.576MX14M.(HL)

HL PASS.PF.600M.X10M/6.2M.

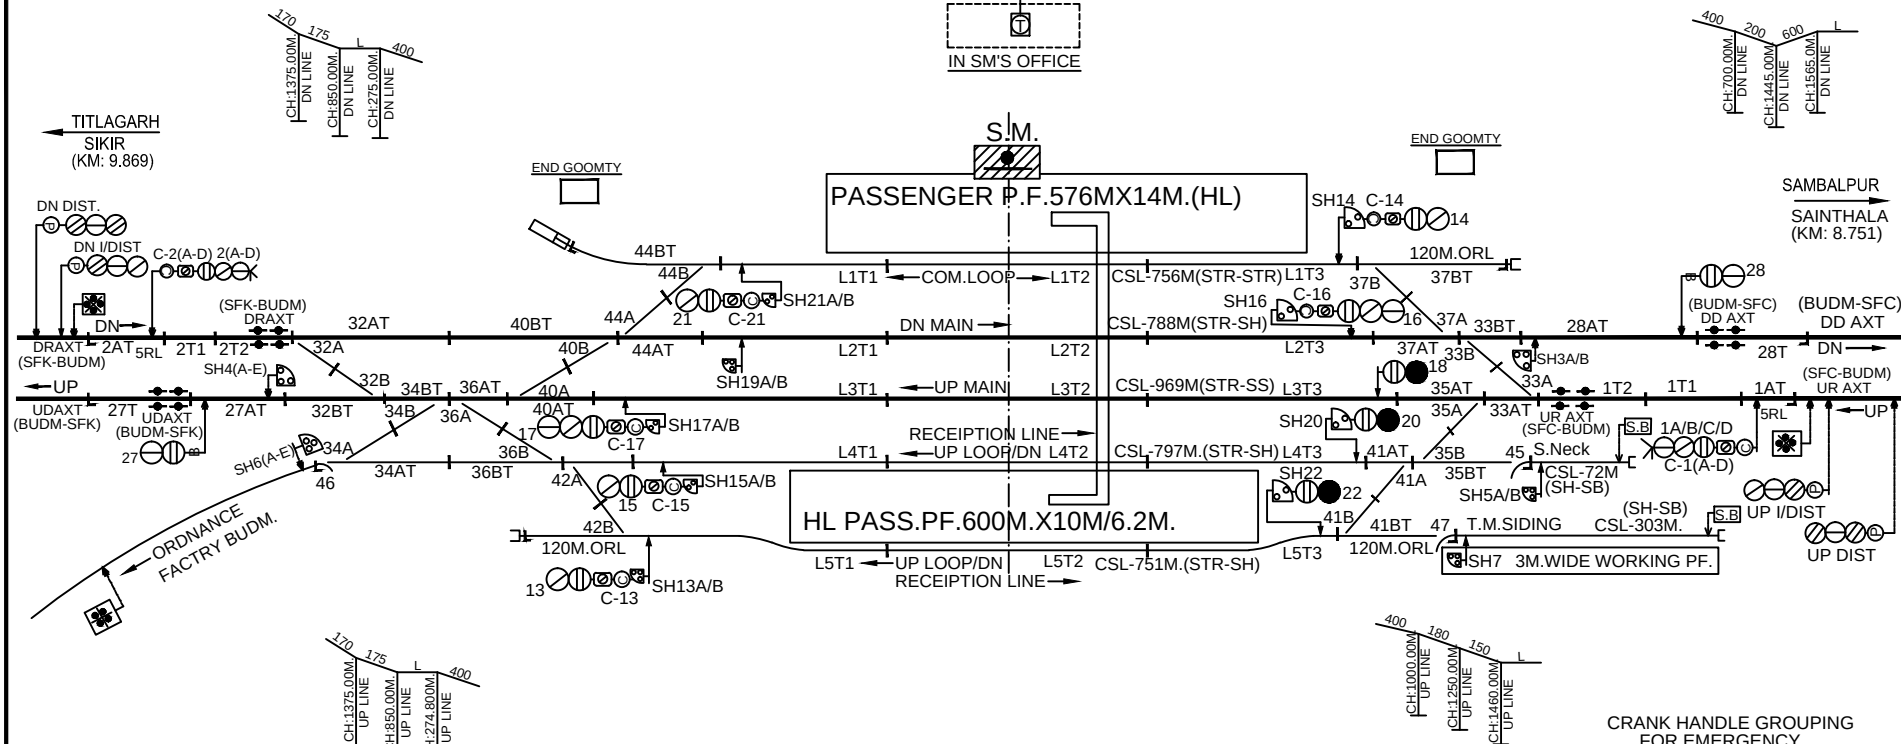

SYSTEM OF WORKING

NO.	SYSTEM	SECTION	INSTRUMENT	LOCATION
1.	ABSOLUTE BLOCK	BADMAL - SIKIR	DLBI(SGE)	S.M.
2.	ABSOLUTE BLOCK	BADMAL - SAINTALA	DLBI(SGE)	S.M.

CONTROL AT S.M. WITH DUAL VDU.

TOTAL NUMBER OF CONTROLS :- 1 TO 50

SIGNAL CONTROL :- 1 TO 30.

SPARE :- 8 -12.23 - 26.29.30.

POINTS & OTHER CONTROLS :- 31 TO 50.


SPARE :- 31.38.39.43.48.49.50.

CRANK HANDLE GROUPING FOR EMERGENCY OPERATION OF POINTS

SL. NO.	CRANK HANDLE	CONTROL POINTS
1.	CH1	33A/B.
2.	CH2	34A/B.35A/B.36A/B.
3.	CH3	37A/B.44A/B.
4.	CH4	32A/B.40A/B.
5.	CH5	41A/B.42A/B.
6.	CH6	45.
7.	CH7	46.
8.	CH8	47.

NM: 08.12.23




DN ASPECT CONTROL CHART

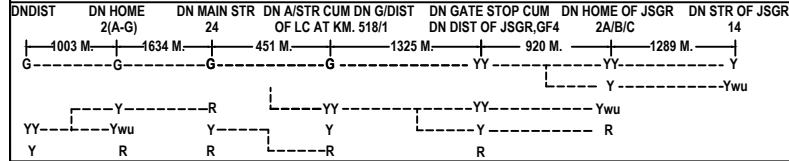

BRUNDAMAL(BXQ)

S.I. No. 22099 ALT-'J',STD:-II R.
KM:520.658 F/HWH,KM:6.414 F/JSGR
KM:520/25-27(UP),KM:520/26-28(DN)

UP / DN

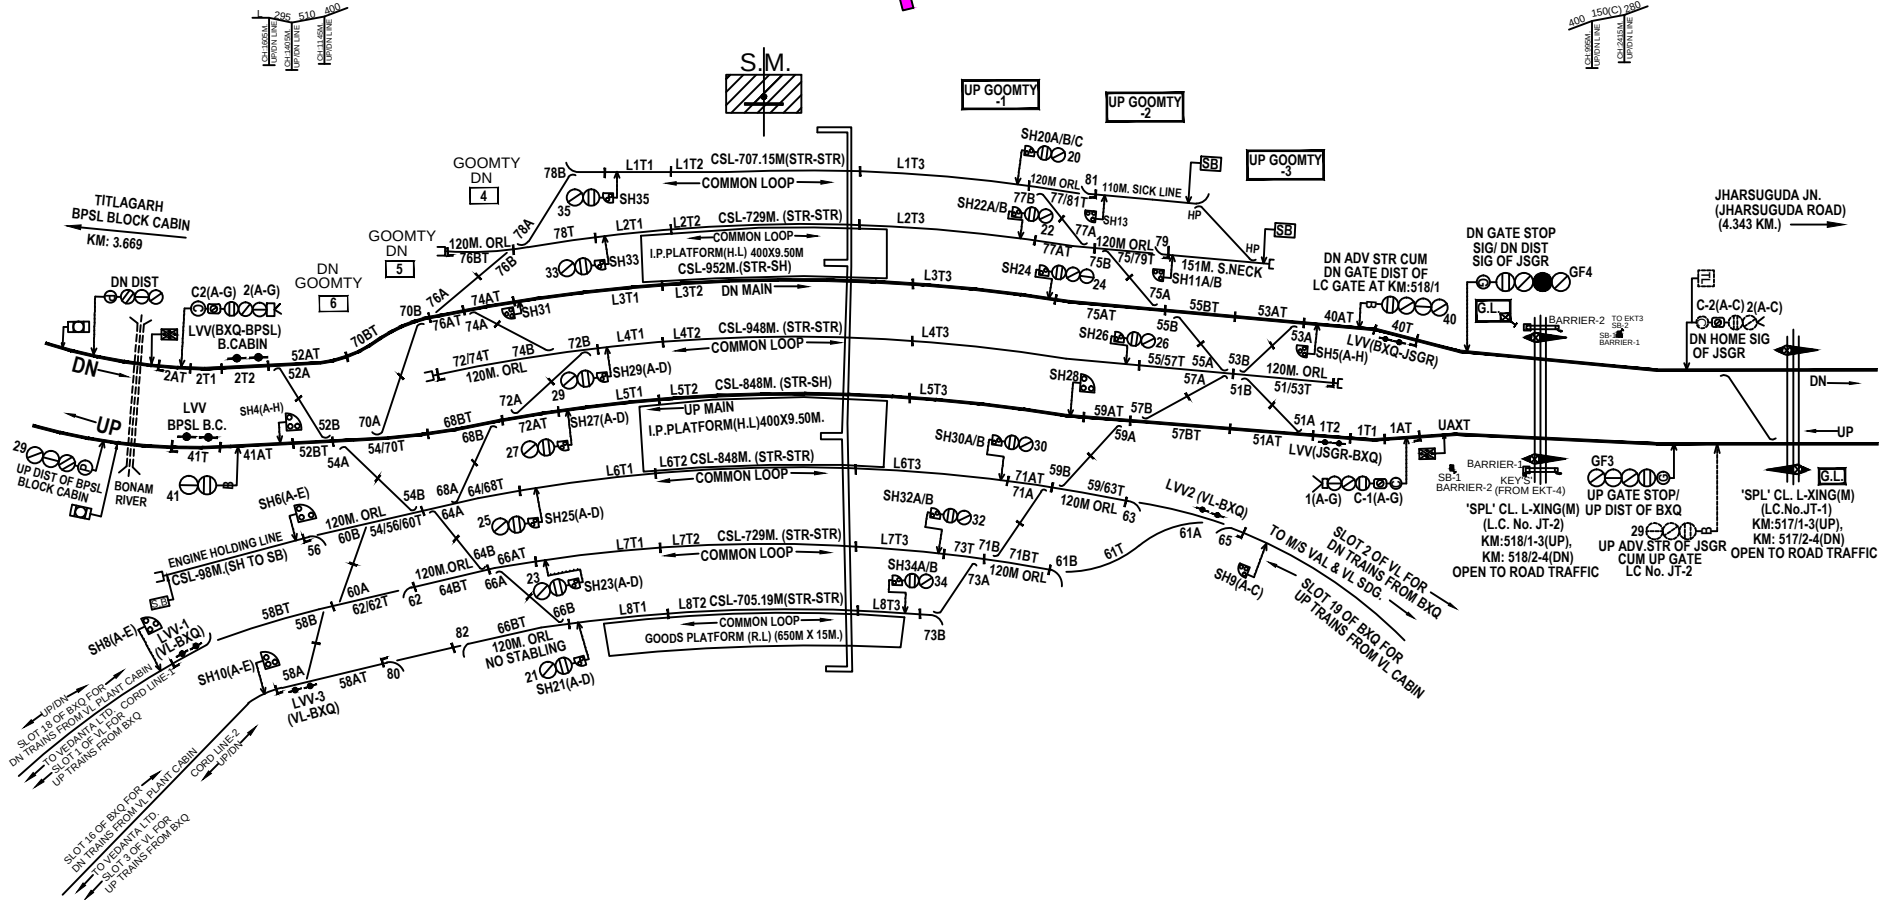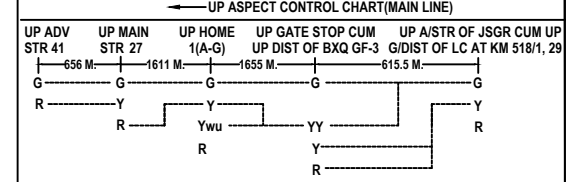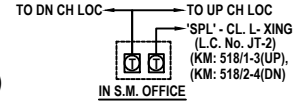


TOTAL NUMBER OF CONTROLS :- 1 TO 100
SIGNAL CONTROL :- 1,2,4,5,6,8,9,10,11,13,16,(20 TO 35),40,41.
POINTS & OTHER CONTROL :- 18,19(50 TO 66),68,(70 - 82)
SPARE :- 3,7,12,14,15,17,36,37,38,39,(42 TO 49)
58,67,69,(83 TO 100).

SYSTEM OF WORKING



NO.	SYSTEM	SECTION	INSTRUMENT	LOCATION
1.	ABSOLUTE BLOCK	BRUNDAMAL-BPSL BLOCK CABIN	DLBI	S.M.
2.	ABSOLUTE BLOCK	BRUNDAMAL-JHARSUGUDA ROAD	DLBI	S.M.
3.	INTER SLOTTING	BRUNDAMAL-VL INPLANT CABIN (CORD LINE - 1 & 2)	INTER SLOTTING WITH LVCD	S.M.

CRANK HANDLE CONTROL FOR EMERGENCY OPERATION OF POINTS					
NO.	CRANK HANDLE	CONTROL POINTS	NO.	CRANK HANDLE	CONTROL POINTS
1.	CH1	51.57	8.	CH8	61.63,65,71,73
2.	CH2	52.70	9.	CH9	62.66,82.
3.	CH3	53.55	10.	CH10	72
4.	CH4	54.68	11.	CH11	74,76
5.	CH5	58.50,80.	12.	CH12	75
6.	CH6	59	13.	CH13	77,79,81
7.	CH7	56.60,64	14.	CH14	78

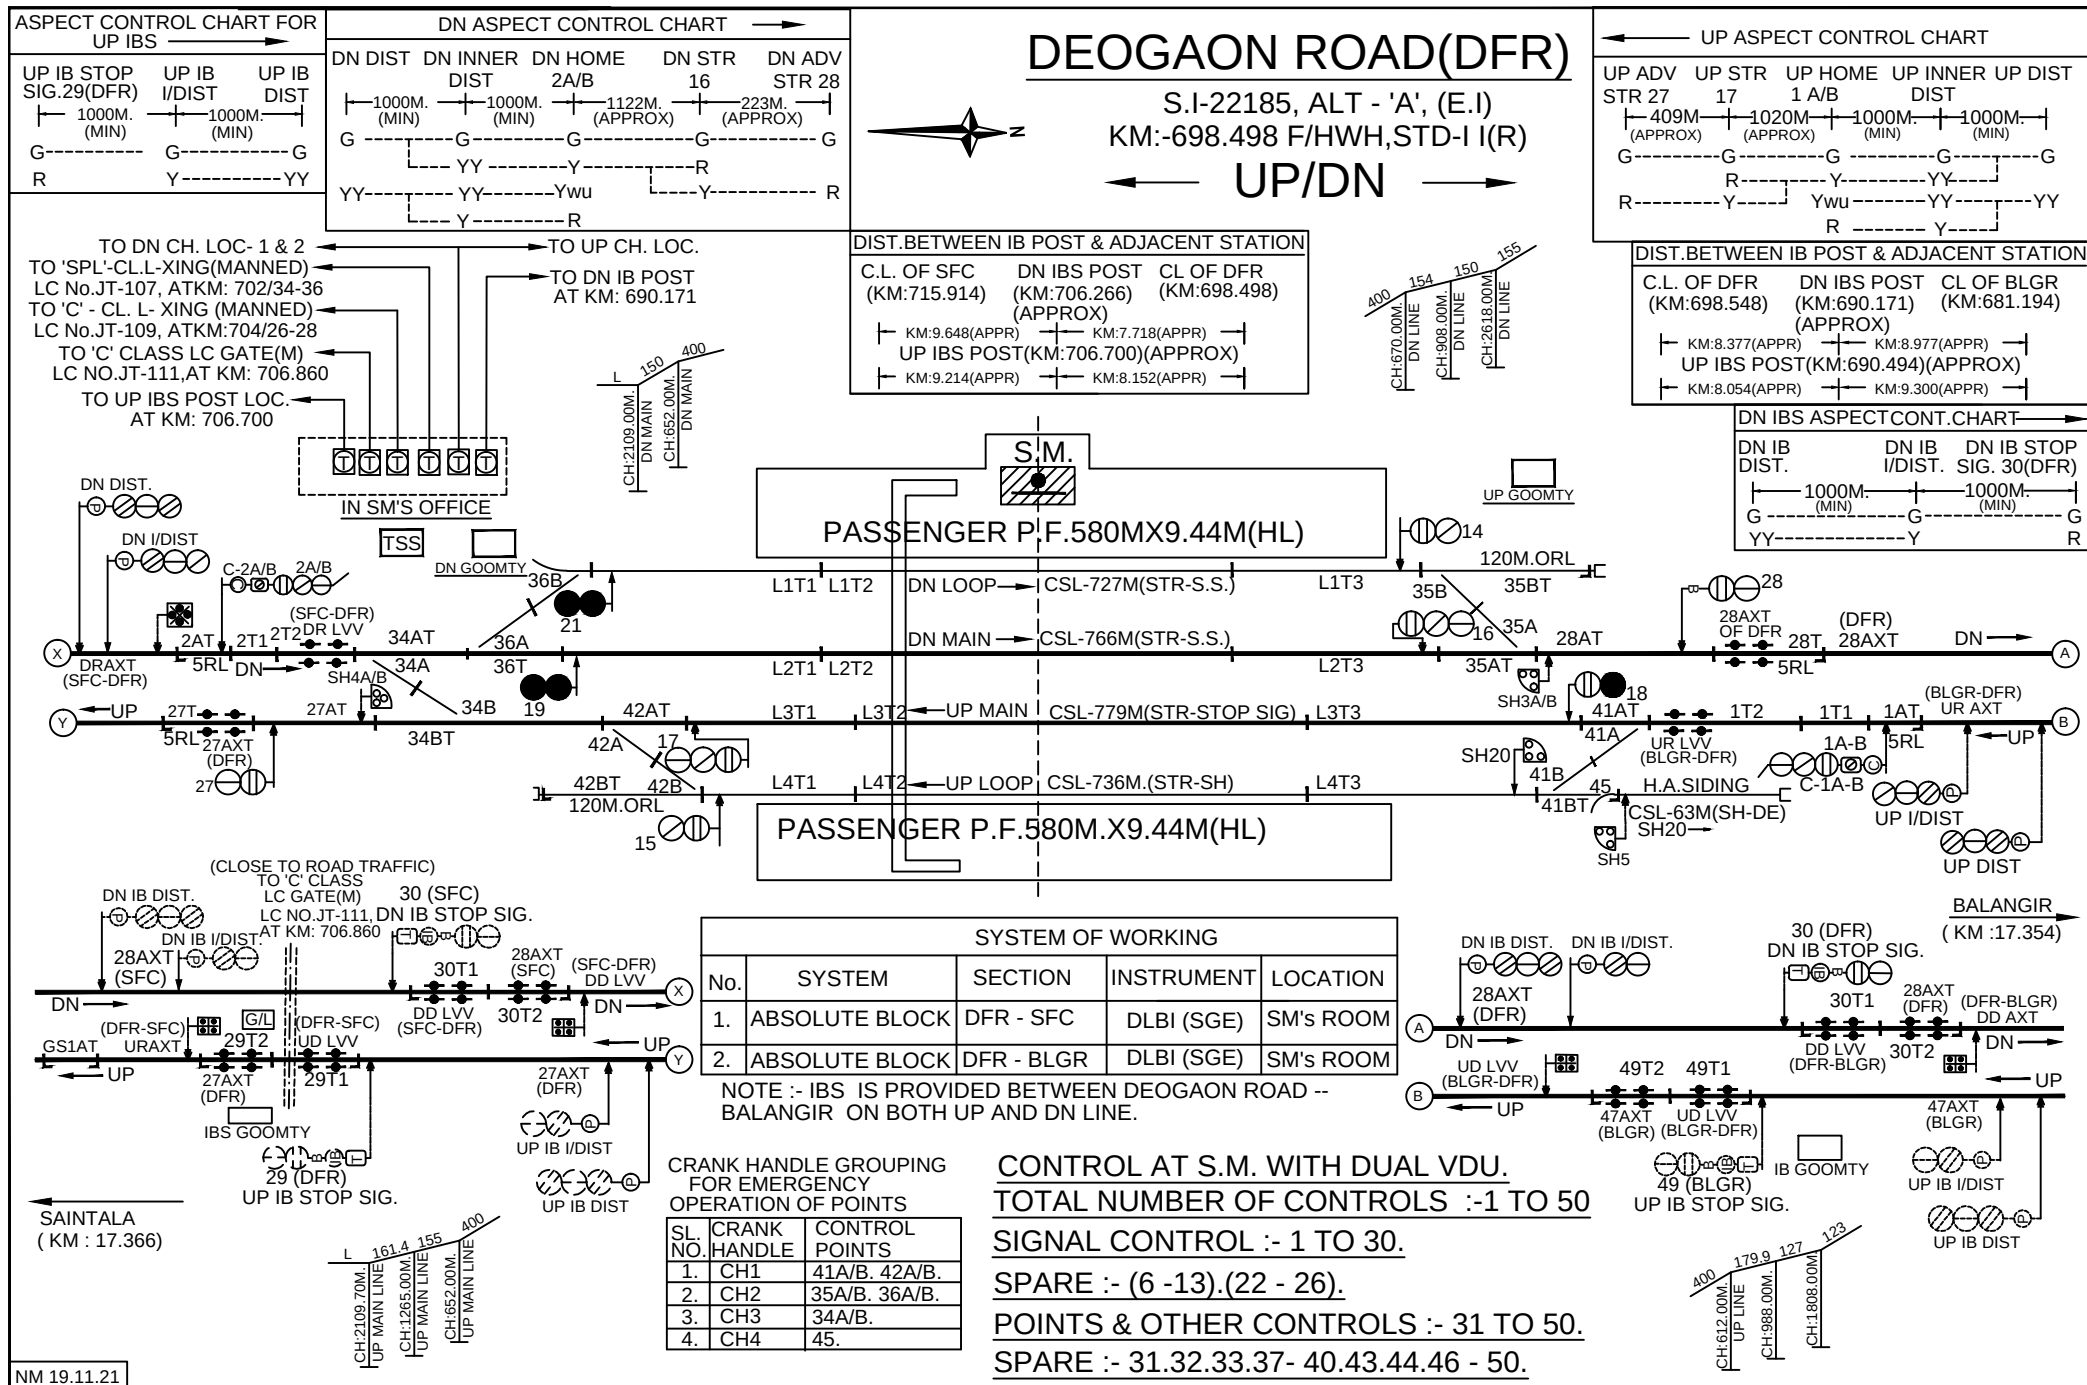



←UP/DN→

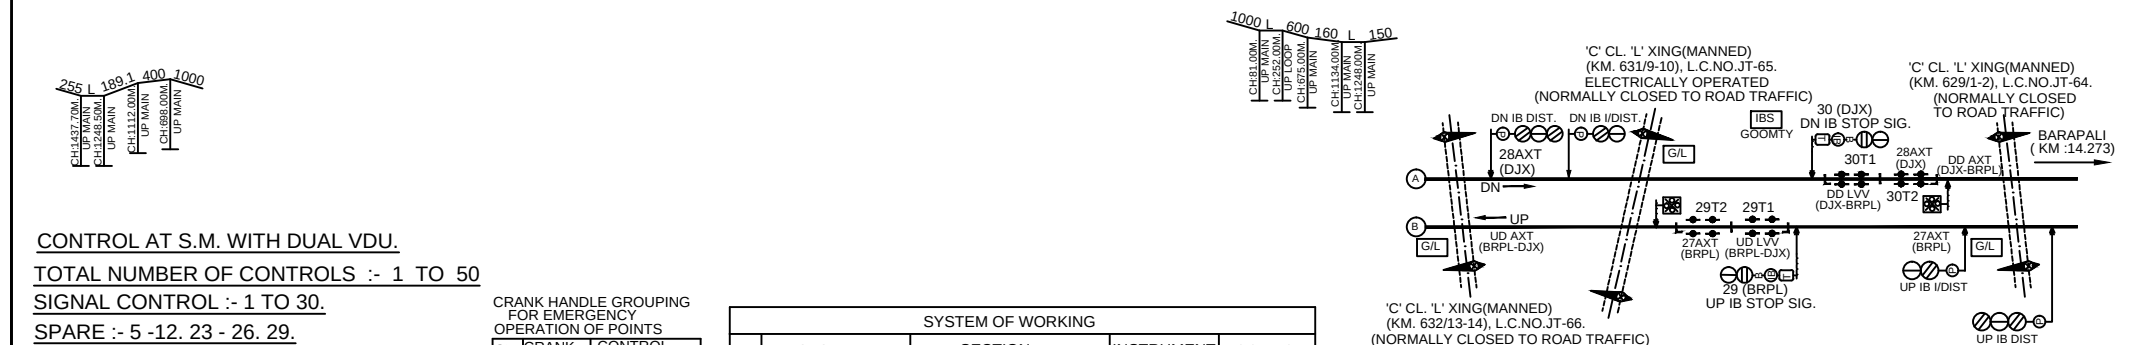
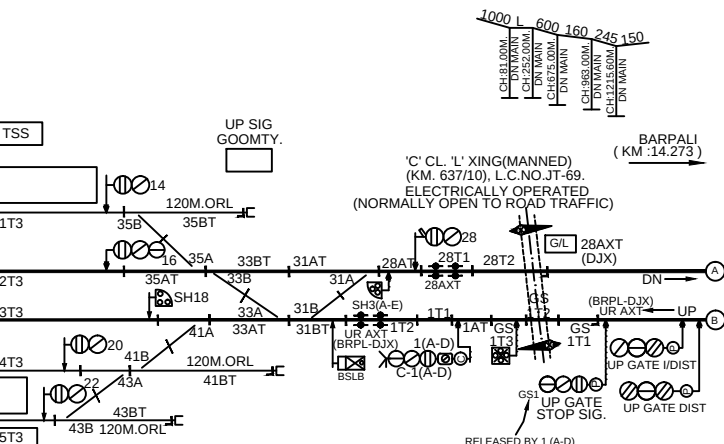


SPARE :- 37.38.39.40.45 - 49.

SL. NO.	CRANK HANDLE	CONTROL POINTS
1.	CH1	31A/B. 33A/B.
2.	CH2	41A/B. 42A/B.
3.	CH3	35A/B. 36A/B.
4.	CH4	32A/B. 34A/B.
5.	CH5	43A/B. 44A/B.

SYSTEM OF WORKING				
No.	SYSTEM	SECTION	INSTRUMENT	LOCATION
1.	ABSOLUTE BLOCK	DUNGRI PALI-BARPALI	DLBI (SGE)	SM's ROOM
2.	ABSOLUTE BLOCK	DUNGRI PALI-KHALIAPALI	DLBI (SGE)	SM's ROOM

NOTE :- IBS IS PROVIDED BETWEEN BARPALI -- DUNGRI PALI SECTION ON BOTH UP AND DN LINE.

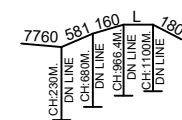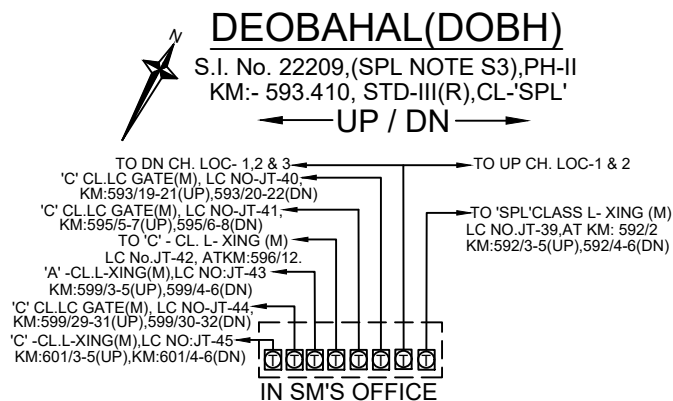

SAMBALPUR
ATTABIRA
(KM : 6.213)


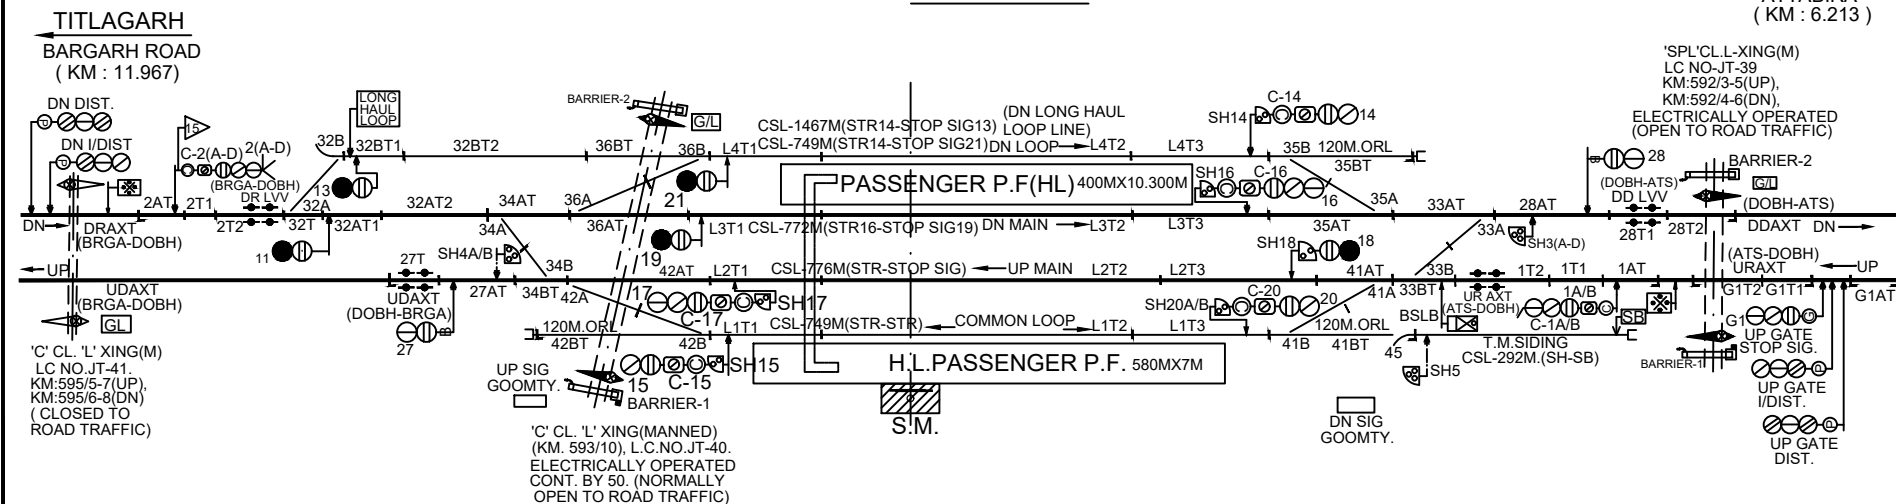


Diagram of a sag vertical curve with a 151' crest length. The curve starts at a 1% grade, rises to a crest, and then descends at a 1% grade. The crest length is 151'. The vertical curve is divided into three segments: 151' / 400' / 7760'. The vertical curve is labeled 'UP LINE' and 'DOWN LINE'.



SL. NO.	CRANK HANDLE	CONTROL POINTS
1.	CH1	33A/B.
2.	CH2	41A/B.42A/B.
3.	CH3	32A/B.35A/B.36A/B.
4.	CH4	34A/B.
5.	CH5	45

TOTAL NUMBER OF CONTROLS :- 1 TO 50
SIGNAL CONTROL :- 1 TO 30.
SPARE :- 6-10.12.22 - 26.29.30.
POINTS & OTHER CONTROLS :- 31 TO 50.
SPARE :- 31.37- 40.43.44.46.47.48.

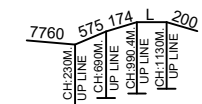

SYSTEM OF WORKING

NO.	SYSTEM	SECTION	INSTRUMENT	LOCATION
1.	ABSOLUTE BLOCK	DEOBAHAL-BARGARH ROAD	DLBI(SGE)	S.M.
2.	ABSOLUTE BLOCK	DEOBAHAL-ATTABIRA	DLBI(SGE)	S.M.

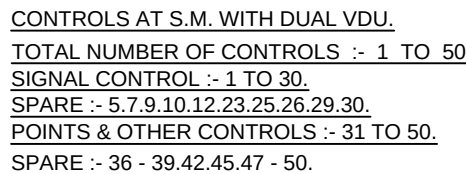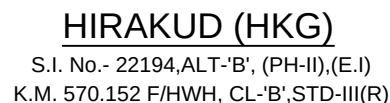

CRANK HANDLE GROUPING FOR EMERGENCY OPERATION OF POINTS		
SL. NO.	CRANK HANDLE	CONTROL POINTS
1.	CH1	31A/B.
2.	CH2	33A/B. 34A/B.
3.	CH3	35A/B. 40A/B.
4.	CH4	41A/B. 42A/B.
5.	CH5	43A/B. 36A/B.
6.	CH6	32A/B.
7.	CH7	46.
8.	CH8	44.

SYSTEM OF WORKING				
NO.	SYSTEM	SECTION	INSTRUMENT	LOCATION
1.	ABSOLUTE BLOCK	HIRAKUD - SAMBALPUR JN.	DLBI(SGE)	S.M.
2.	ABSOLUTE BLOCK	HIRAKUD - GODBHAGA	DLBI(SGE)	S.M.





JHARSUGUDA ROAD(JSGR)

S.I. No. 22113 ALT-'E'.

KM:- 516.316 F/HWH

CL - 'B',STD -II(R)

UP/DN

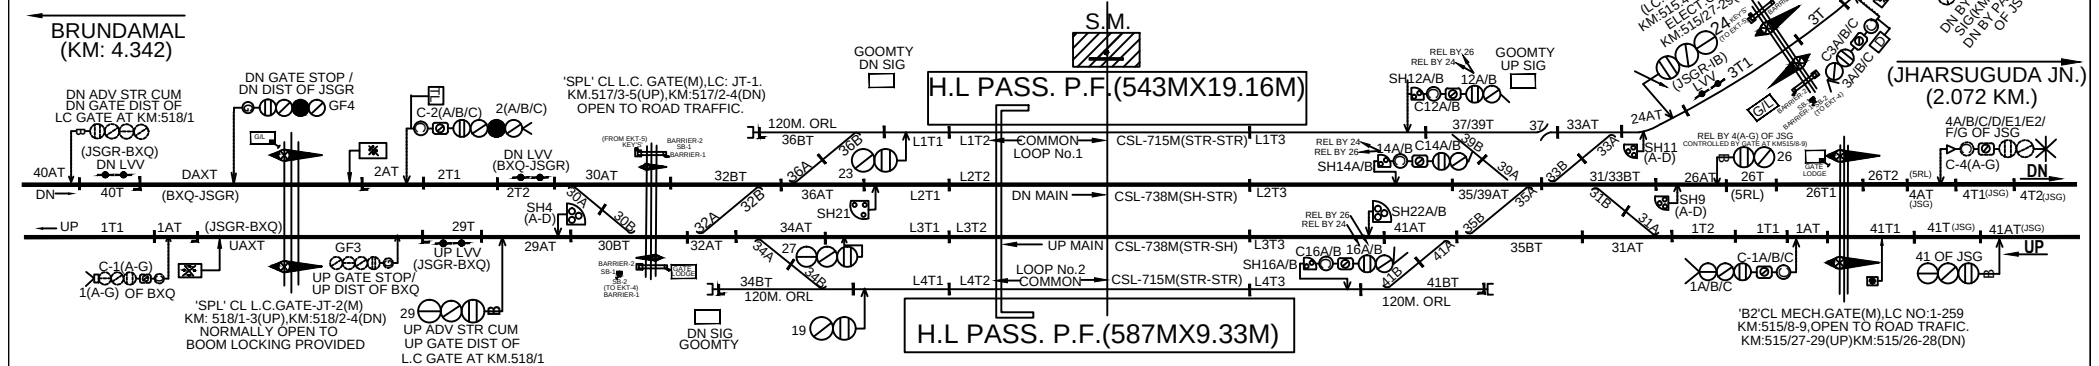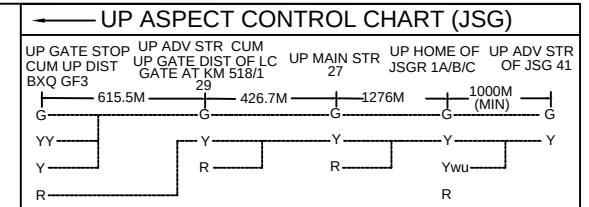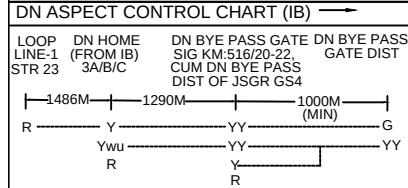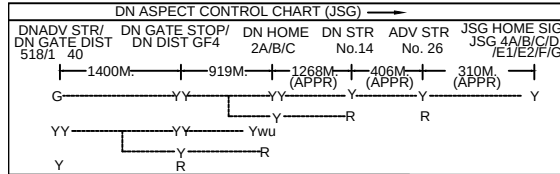

SYSTEM OF WORKING

NO.	SYSTEM	SECTION	INSTRUMENT	LOCATION
1.	ABSOLUTE BLOCK	JHARSUGUDA ROAD JN - IB	TLBI(DIADO)	S.M.
2.	ABSOLUTE BLOCK	JHARSUGUDA ROAD JN - BRUNDAMAL	DLBI	S.M.
2.	ABSOLUTE BLOCK	JHARSUGUDA ROAD JN - JHARSUGUDA JN	DLBI	S.M.

CONTROL PANEL IN S.M.

TOTAL NUMBER OF CONTROLS :- 1 TO 60


SIGNAL CONTROLS :- 1,2,3,4,9,11,12,14,16,19,21,22,23,24,26,27,29


POINT & OTHER CONTROLS :- 30,31,32,33,34,35,36,37,39,41,56,57,59

SPARE :- 5,6,7,8,10,13,15,17,18,20,25,28,38,40,(42-55),58,60.

CRANK HANDLE CONTROL FOR EMERGENCY OPERATION OF POINTS

NO.	CH	POINT
1.	CH1	36, 38.
2.	CH2	30, 32.
3.	CH3	34, 41.
4.	CH4	31, 35.
5.	CH5	33.
6.	CH6	37.

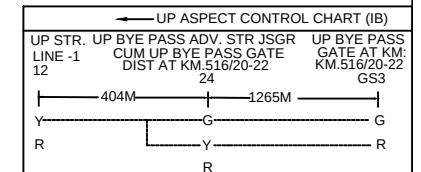

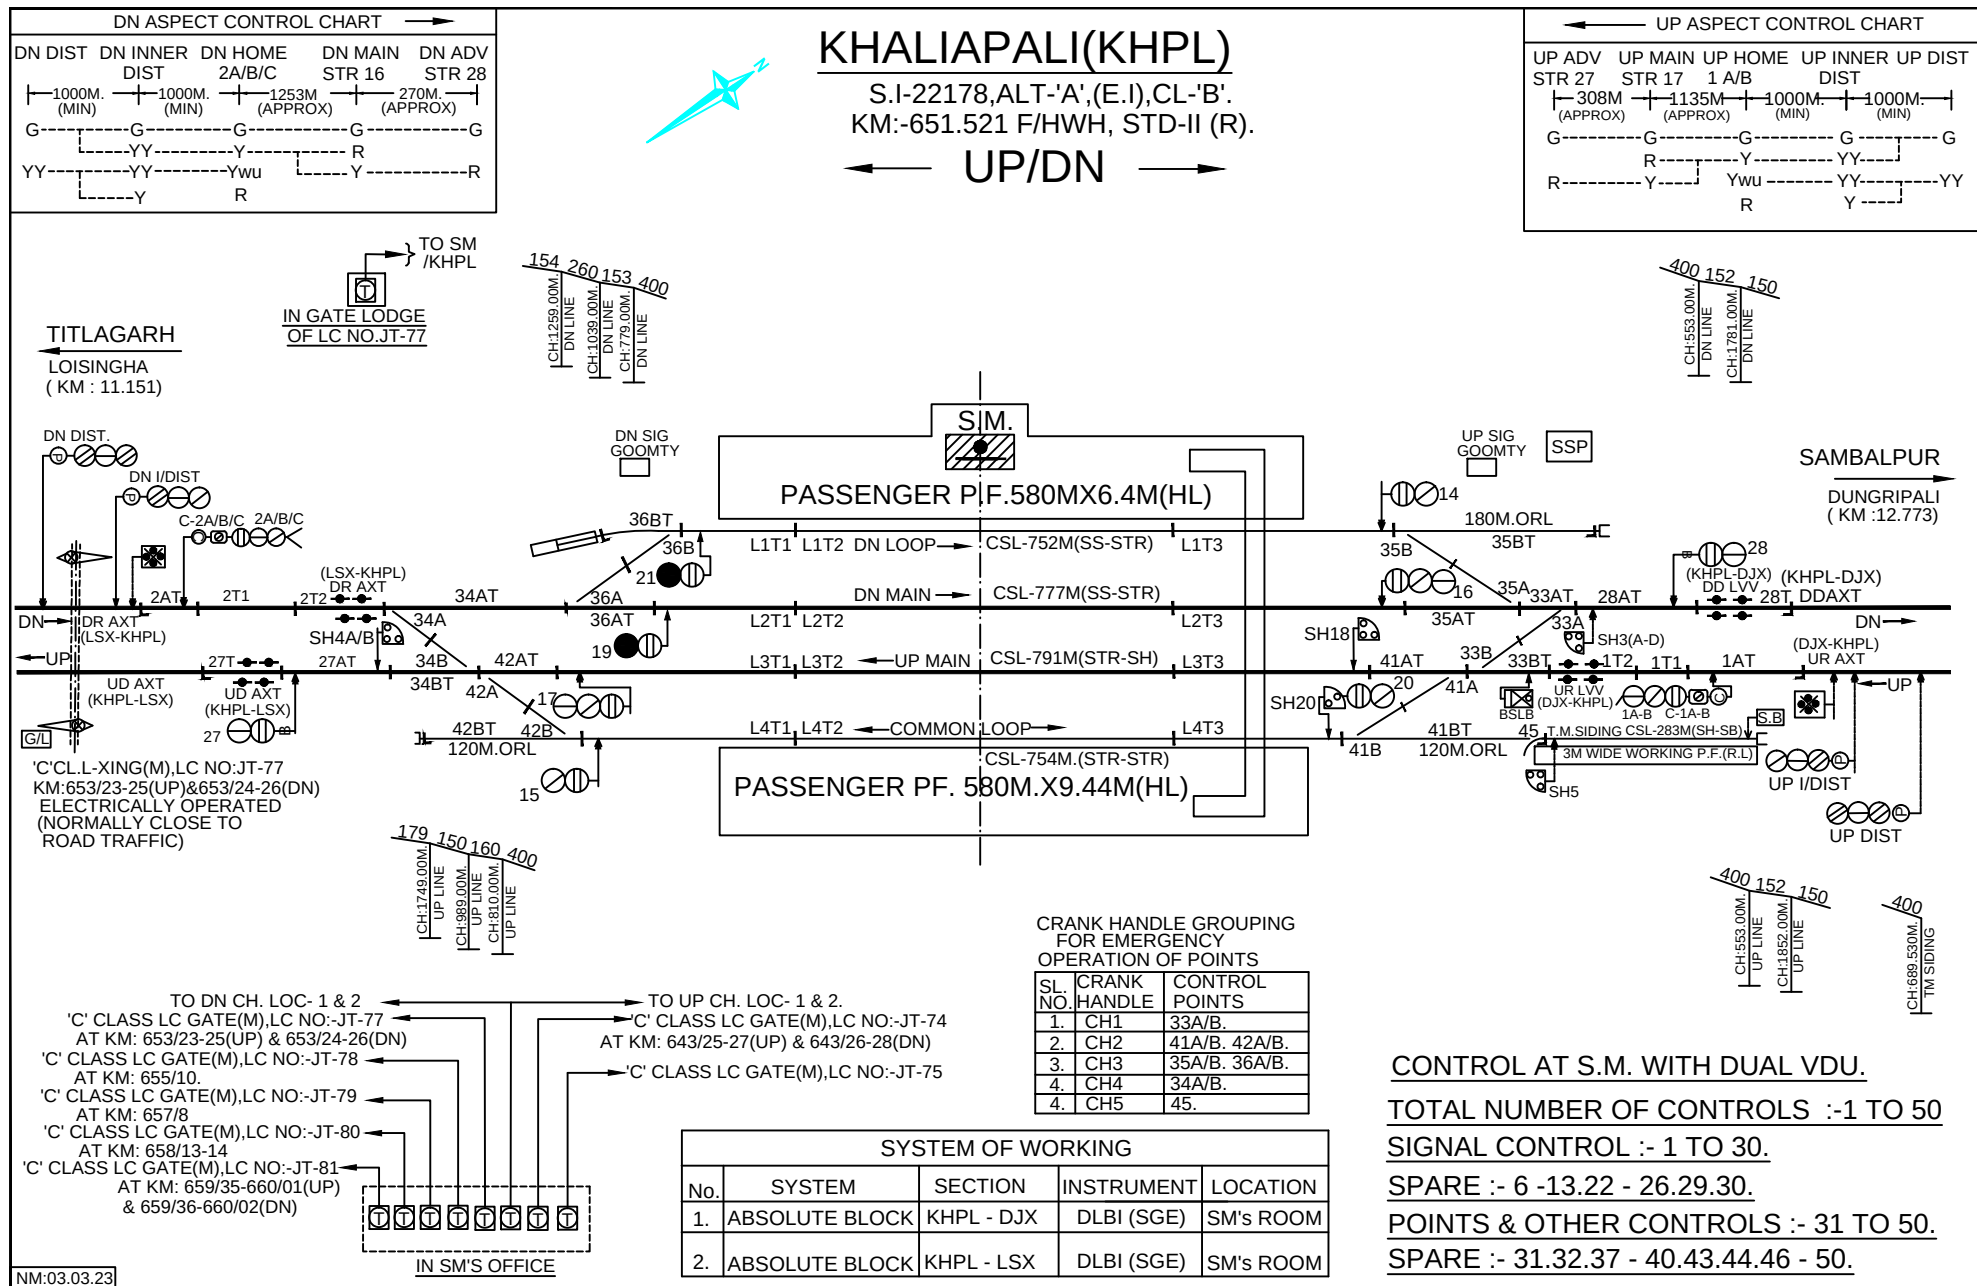

CONTROL AT S.M. WITH DUAL VDU.


TOTAL NUMBER OF CONTROLS :-1 TO 50


SIGNAL CONTROL :- 1 TO 30.

SPARE :- 6 -13.22 - 26.29.30.

POINTS & OTHER CONTROLS :- 31 TO 50.

SPARE :- 31.32.37 - 40.43.44.46 - 50.




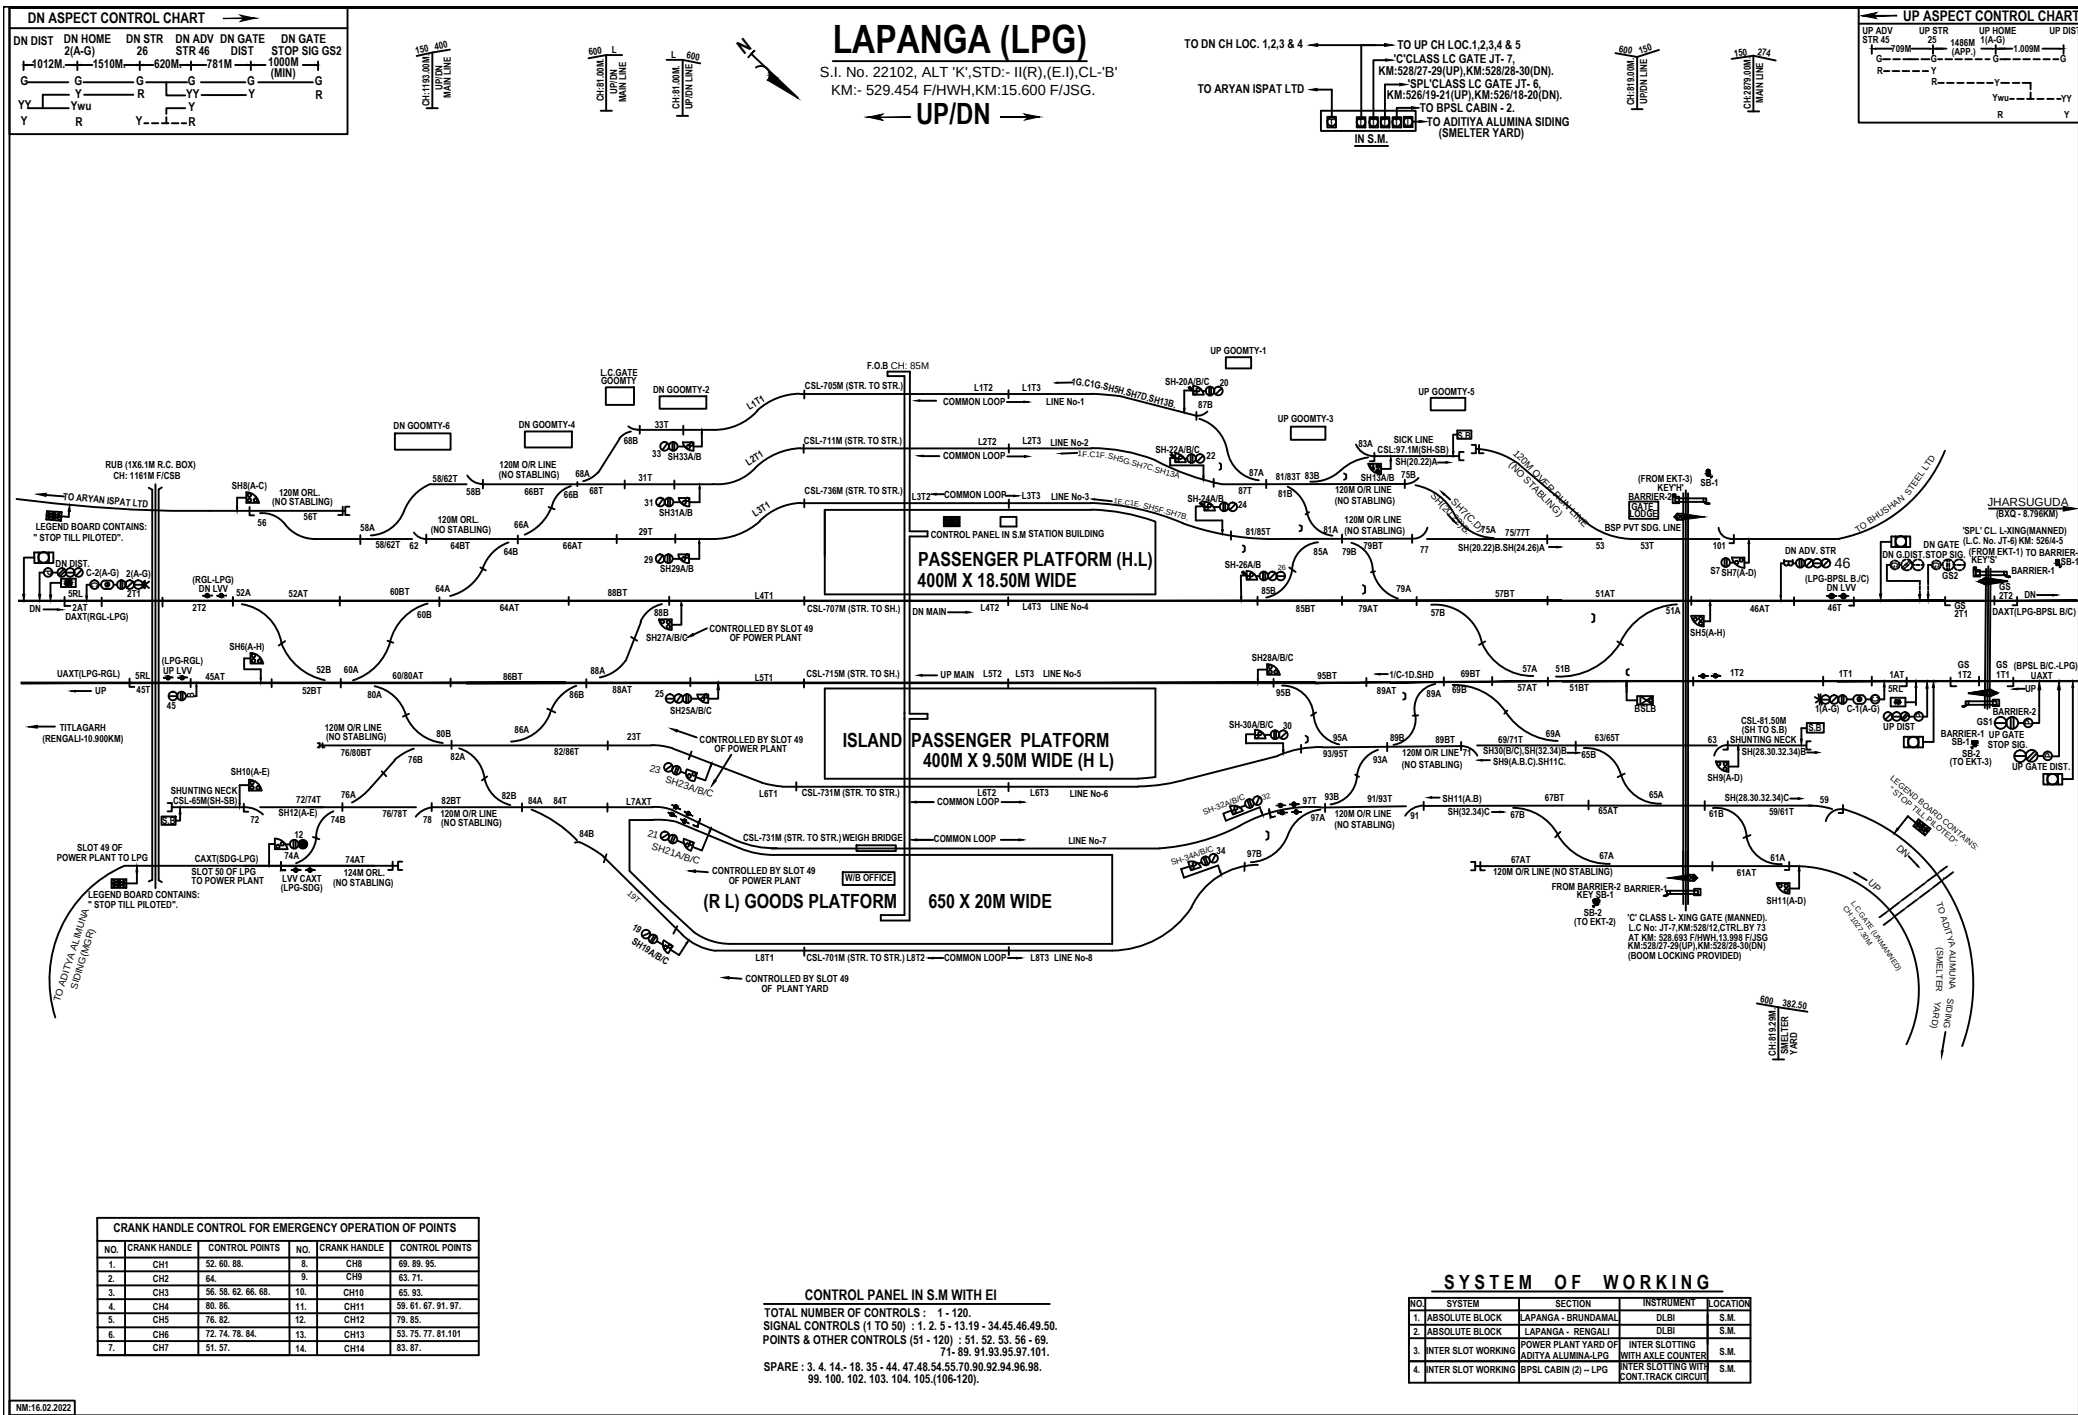


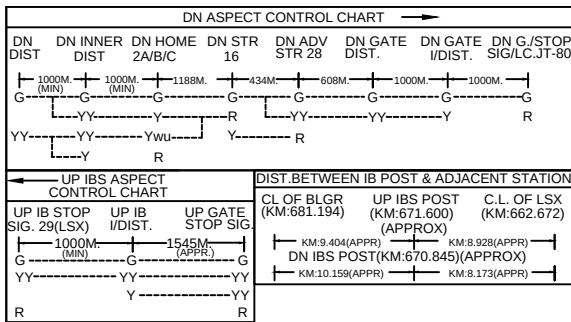


LOISINGHA (LSX)

S.I-22201,ALT-'A', (E.I)
KM:-662.672/HWH. STD-I I (R),CL-'B'.

UP/DN

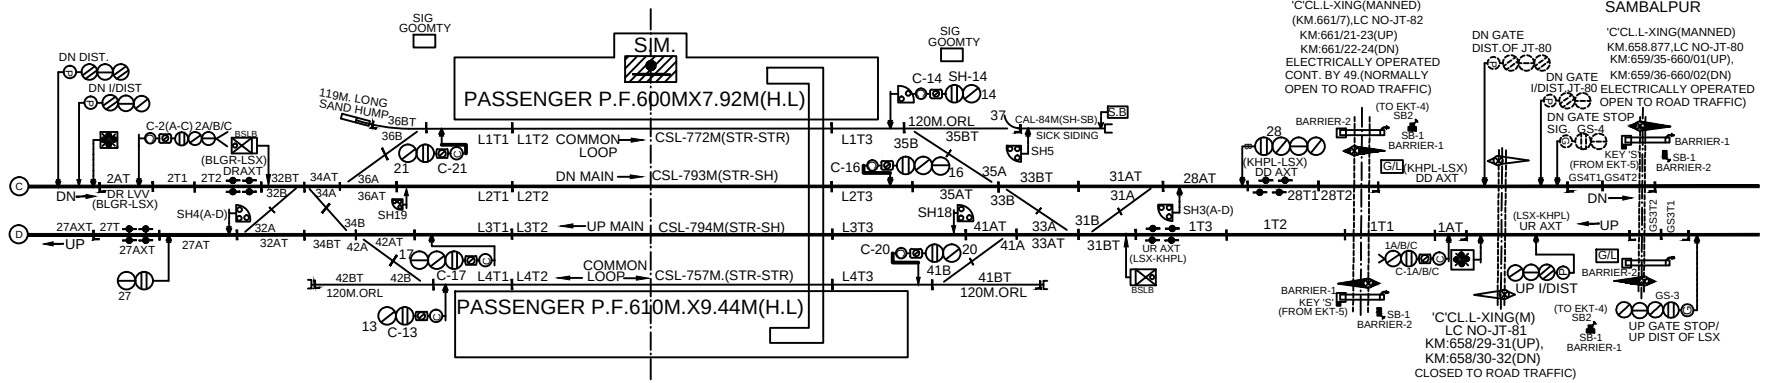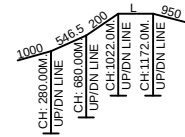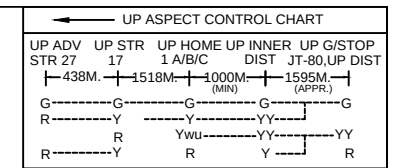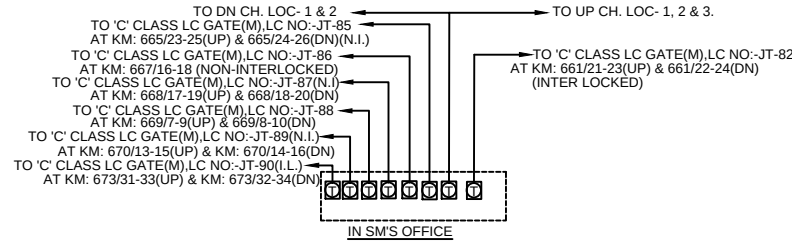

TITLAGARH
BALANGIR
(KM : 18.614)

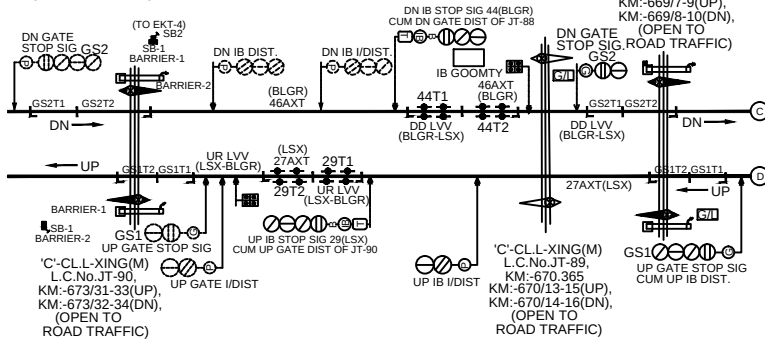

SAMBALPUR
LOISINGHA
(KM : 19.104)

CONTROL AT S.M. WITH DUAL VDU.

TOTAL NUMBER OF CONTROLS :- 1 TO 50

SIGNAL CONTROL :- 1 TO 30.

SPARE :- 6 - 12.15.22 - 26.29.30.

POINTS & OTHER CONTROLS :- 31 TO 50.

SPARE :- 38.39.40.43.44.45.46.47.48.50.



CRANK HANDLE GROUPING
FOR EMERGENCY
OPERATION OF POINTS

SL	CRANK HANDLE	CONTROL POINTS
1.	CH1	31A/B, 33A/B.
2.	CH2	41A/B, 42A/B.
3.	CH3	35A/B, 36A/B.
4.	CH4	32A/B, 34A/B.
5.	CH5	37.

SYSTEM OF WORKING

No.	SYSTEM	SECTION	INSTRUMENT	LOCATION
1.	ABSOLUTE BLOCK	LSX - BLGR	DLBI (SGE)	SM's ROOM
2.	ABSOLUTE BLOCK	LSX - KHPL	DLBI (SGE)	SM's ROOM

NOTE :- IBS IS PROVIDED BETWEEN LSX - BLGR SECTION ON BOTH UP AND DN LINES.

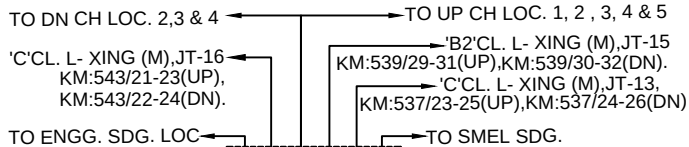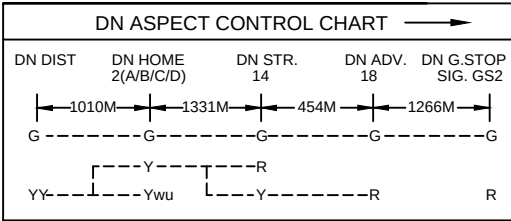




IN SM'S OFFICE

RENGALI (RGL)

S.I. No. 22109 ALT 'G&H',STD:- II(R),(E.I)CL-'B'

KM:-540.355 F/HWH,KM:25.750 F/JSG.

UP/DN

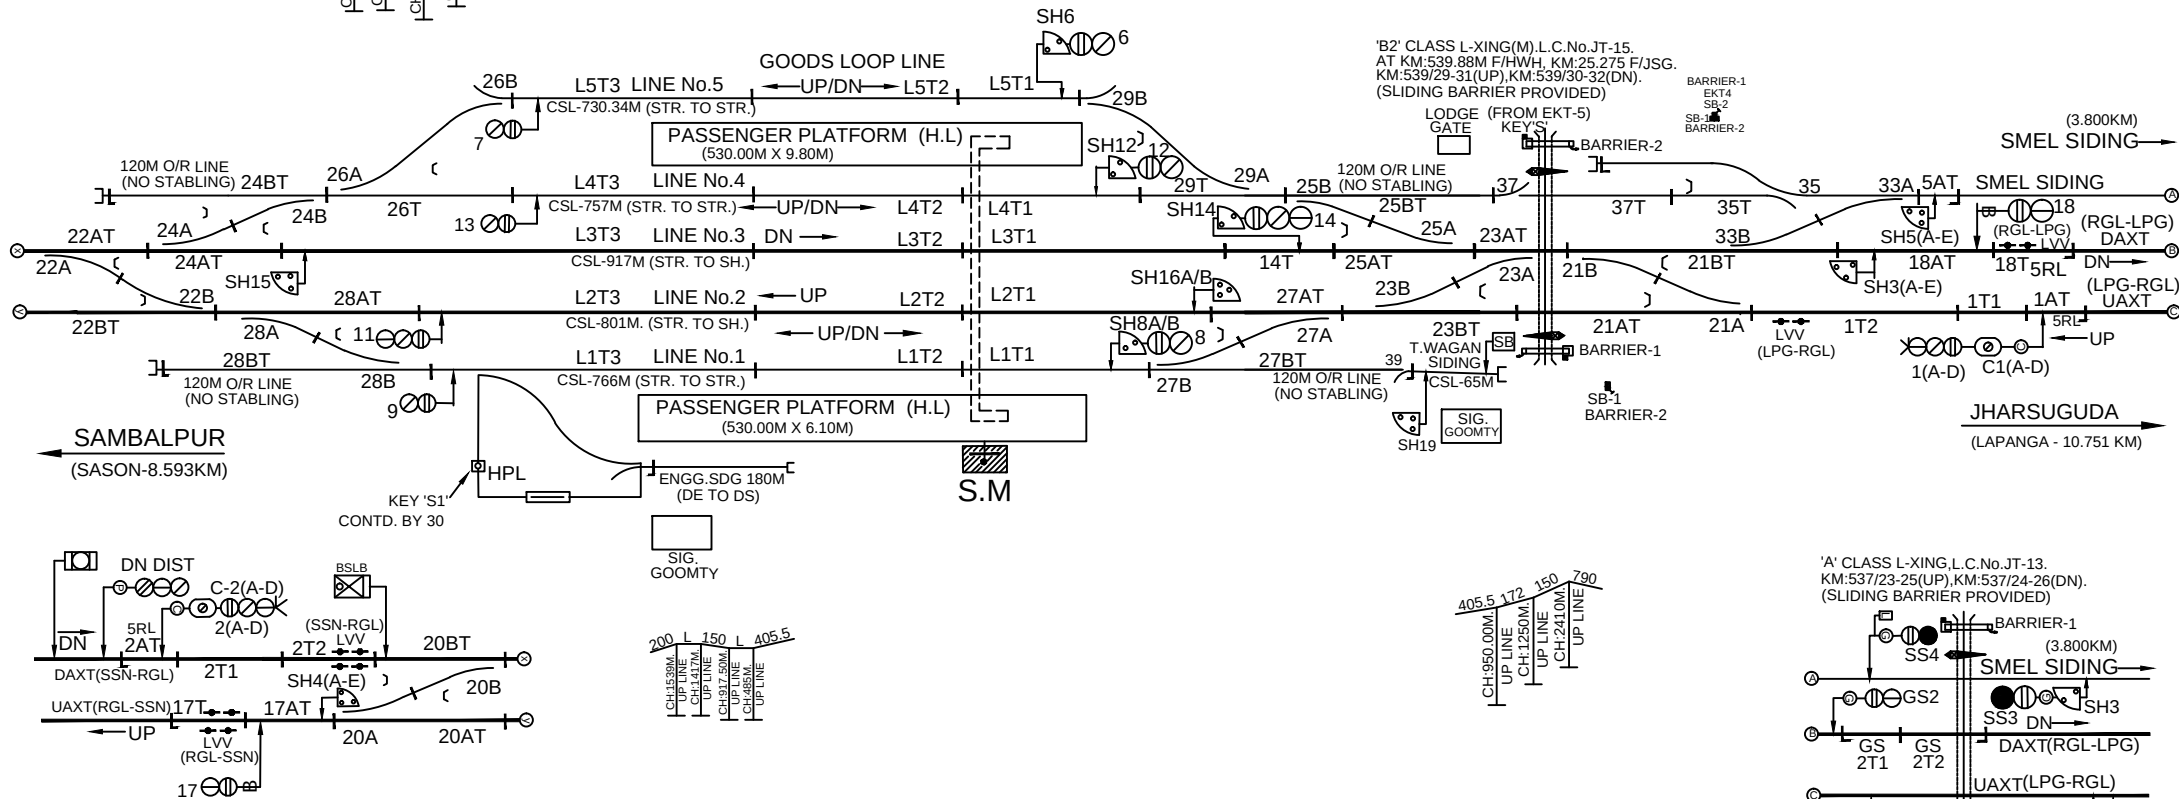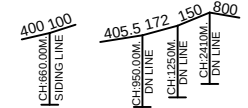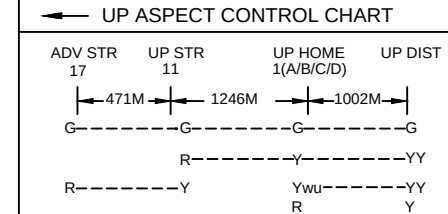

CRANK HANDLE GROUPING FOR
EMERGENCY HAND OPERATION OF POINTS

SL NO.	CRANK HANDLE	CONTROL POINTS
1.	CH1	20, 22.
2.	CH2	21, 23.
3.	CH3	24, 25, 33
4.	CH4	27, 28.
5.	CH5	26, 29.
6.	CH6	35, 37.
7.	CH7	39.

CONTROL PANEL IN S.M.

TOTAL NUMBER OF CONTROLS : 1 - 50

SIGNAL CONTROLS : 1TO 9.11 TO 19.


POINTS & OTHER CONTROLS : 20 TO 31. 33. 35. 37.39.

SPARES : 10. 32. 34. 36. 38.(40-50).

SYSTEM OF WORKING





NO.	SYSTEM	SECTION	INSTRUMENT	LOCATION
1.	ABSOLUTE BLOCK	RENGALI - SASON	DLBI	S.M.
2.	ABSOLUTE BLOCK	RENGALI - LAPANGA	DLBI	S.M.

NM:21.04.2023

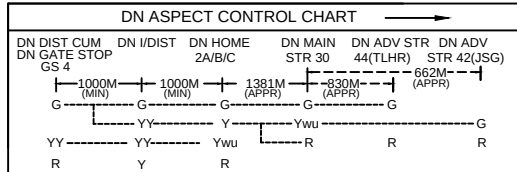

SAMBALPUR JN.(SBP)
S.I. 22197,ALT-'B', STD-II(R),
KM:- 562.900,E.I.,CLASS- 'B'.

← UP / DN →

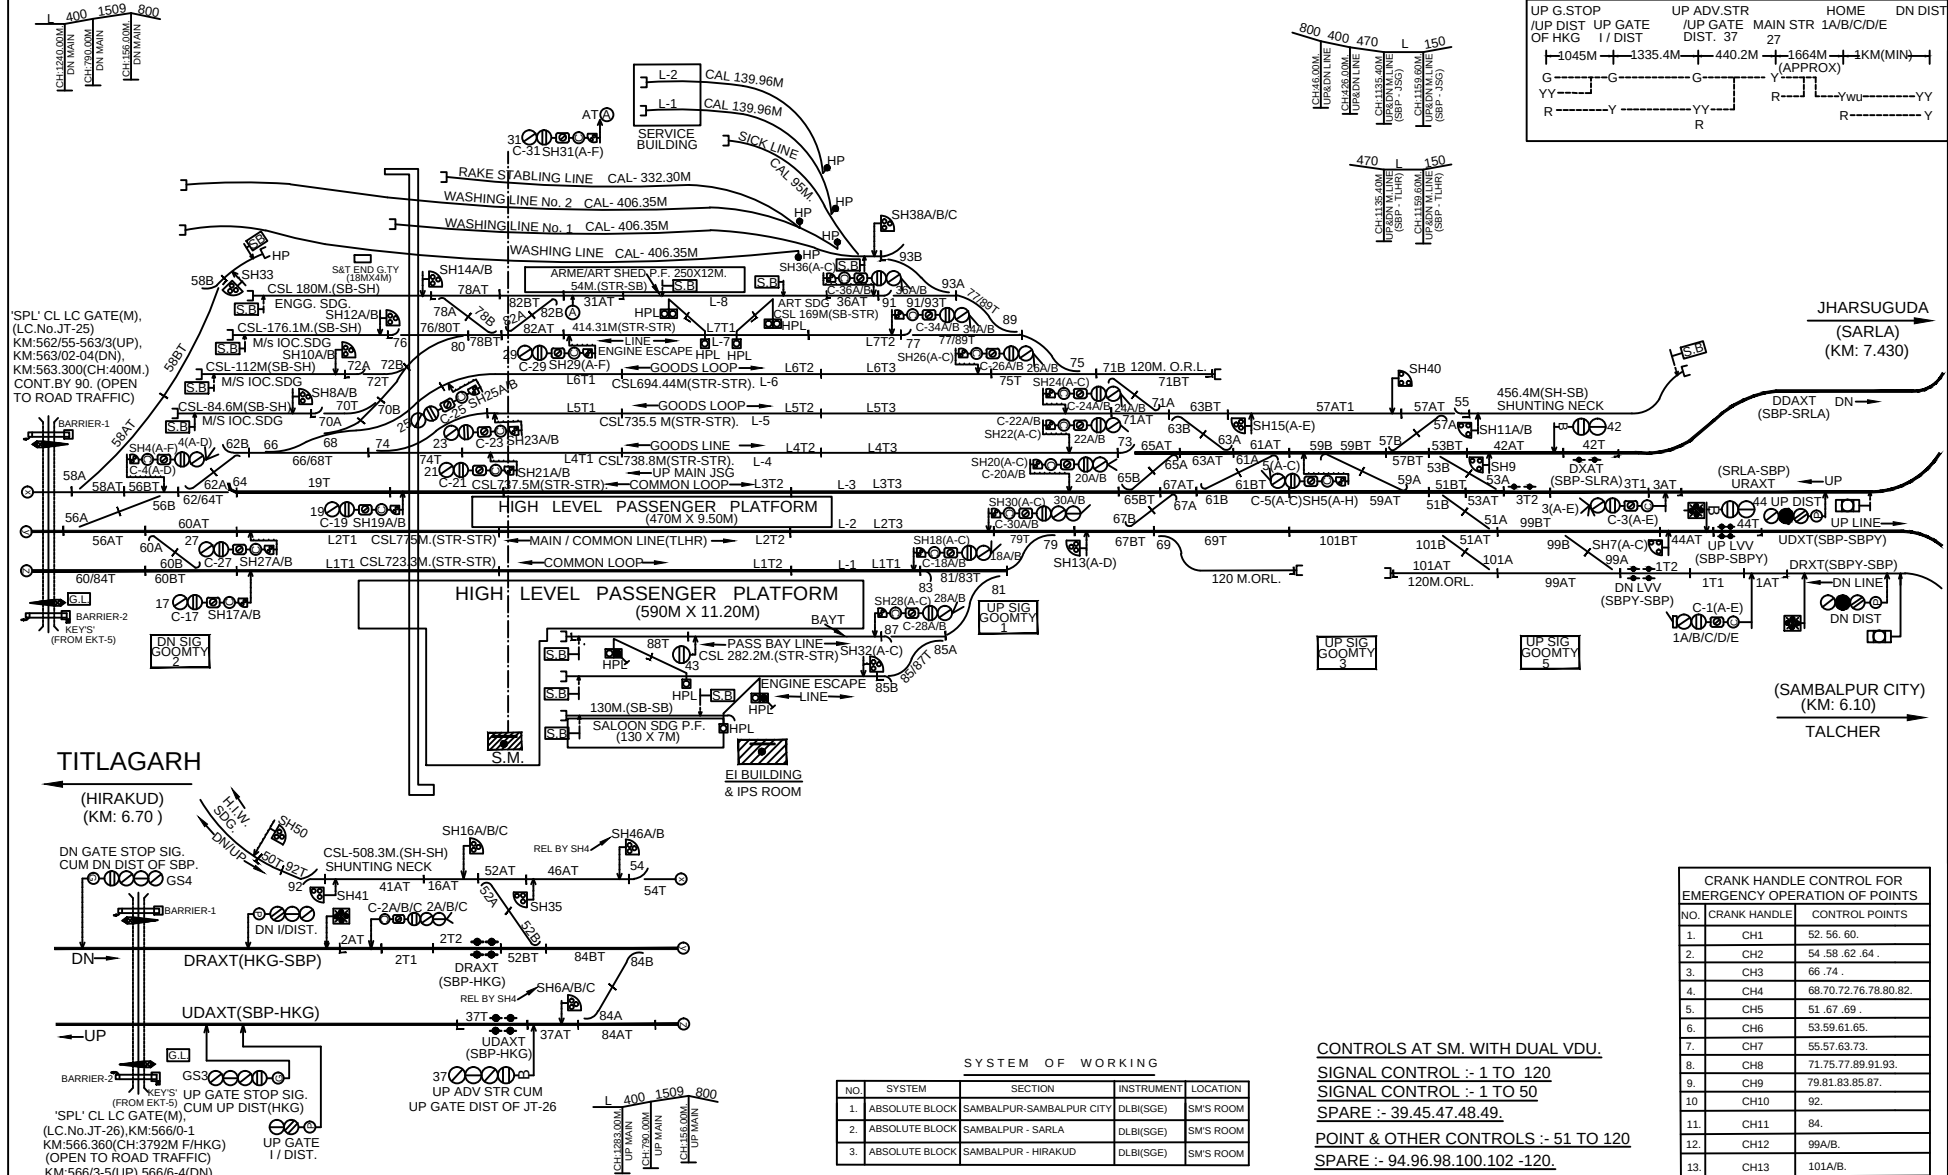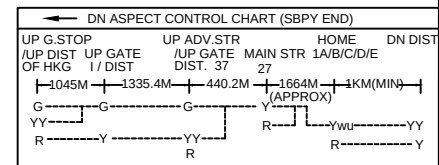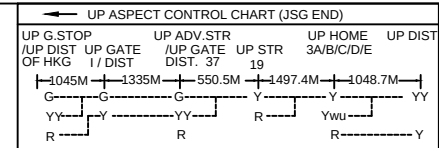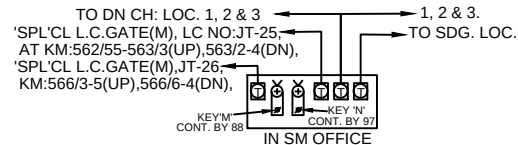


CRANK HANDLE CONTROL FOR EMERGENCY OPERATION OF POINTS		
NO.	CRANK HANDLE	CONTROL POINTS
1.	CH1	52.56.60.
2.	CH2	54.58.62.64.
3.	CH3	66.74.
4.	CH4	68.70.72.76.78.80.82.
5.	CH5	51.67.69.
6.	CH6	53.59.61.65.
7.	CH7	55.57.63.73.
8.	CH8	71.75.77.89.91.93.
9.	CH9	79.81.83.85.87.
10.	CH10	92.
11.	CH11	84.
12.	CH12	99A/B.
13.	CH13	101A/B.

SYSTEM OF WORKING			
NO.	SYSTEM	SECTION	INSTRUMENT LOCATION
1.	ABSOLUTE BLOCK	SAMBALPUR-SAMBALPUR CITY	DLBI(SGE) SM'S ROOM
2.	ABSOLUTE BLOCK	SAMBALPUR - SARLA	DLBI(SGE) SM'S ROOM
3.	ABSOLUTE BLOCK	SAMBALPUR - HIRAKUD	DLBI(SGE) SM'S ROOM


CONTROLS AT SM. WITH DUAL VDU.
SIGNAL CONTROL :- 1 TO 120
SIGNAL CONTROL :- 1 TO 50
SPARE :- 39.45.47.48.49.
POINT & OTHER CONTROLS :- 51 TO 120
SPARE :- 94.96.98.100.102 -120.

NM:17.11.23

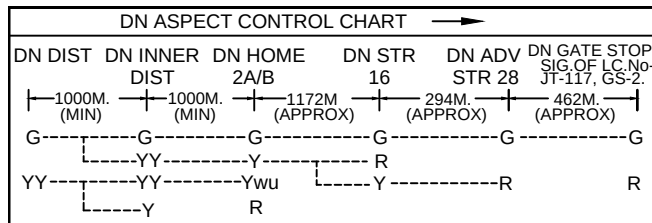

DIST. BETWEEN IB POST & ADJACENT STATION

C.L. OF SFC (KM:715.914)	DN IBS POST (KM:706.266) (APPROX)	CL OF DFR (KM:698.498) (APPROX)
KM:9.648 (APPR)	KM:7.718 (APPR)	
UP IBS POST (KM:706.680) (APPROX)		KM:8.152 (APPROX)

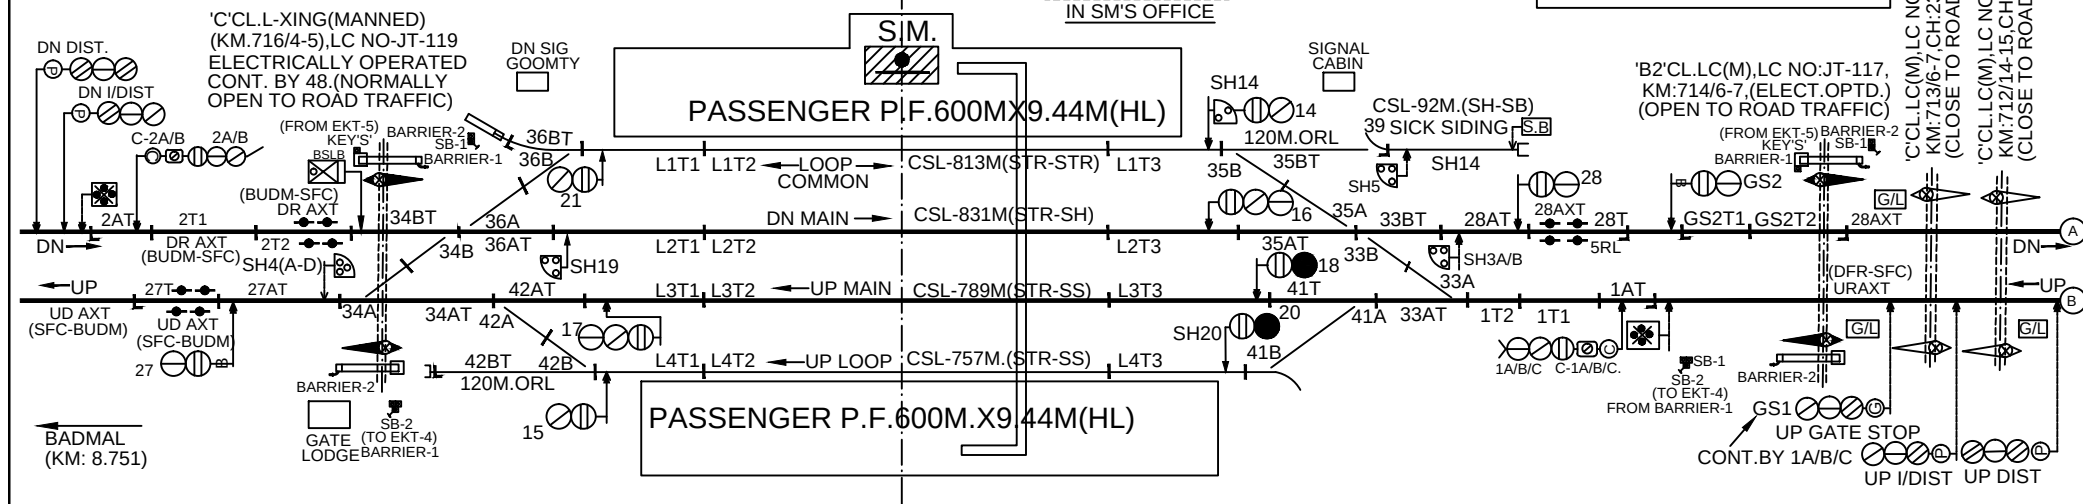




CRANK HANDLE GROUPING FOR EMERGENCY OPERATION OF POINTS


SL. NO.	CRANK HANDLE	CONTROL POINTS
1.	CH1	33A/B.
2.	CH2	41A/B. 42A/B.
3.	CH3	35A/B. 36A/B.
4.	CH4	34A/B.
5.	CH5	39.

SYSTEM OF WORKING




No.	SYSTEM	SECTION	INSTRUMENT	LOCATION
1.	ABSOLUTE BLOCK	SFC-DFR	DLBI (SGE)	SM's ROOM
2.	ABSOLUTE BLOCK	SFC-BUDM	DLBI (SGE)	SM's ROOM

CONTROL AT S.M. WITH DUAL VDU.
TOTAL NUMBER OF CONTROLS :- 1 TO 50
SIGNAL CONTROL :- 1 TO 30.
SPARE :- 6 -13.22 - 26.29.
POINTS & OTHER CONTROLS :- 31 TO 50.
SPARE :- 31.32.37.38.40.43-47.49.50.

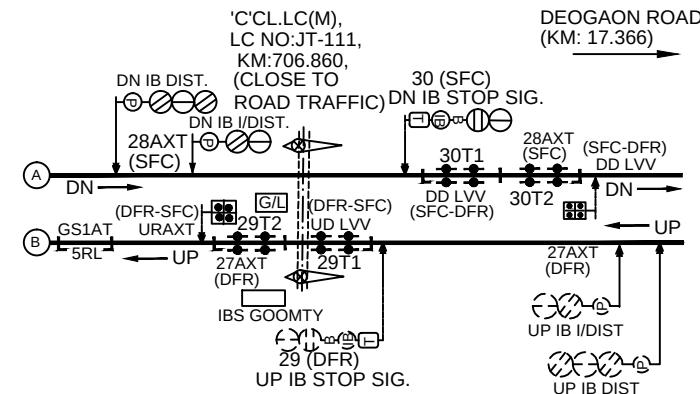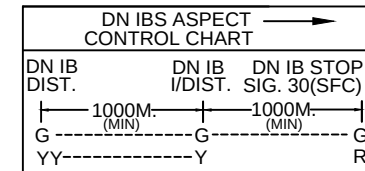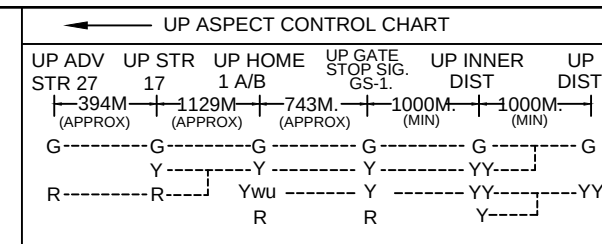

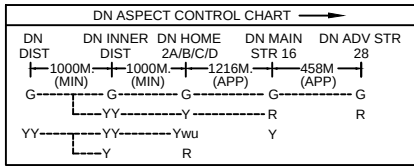

SIKIR(SFK) S.I. NO. 22227, (PH-II), (E.I.) KM:- 734.534 F/HWH, STD-III(R), CL-'B'. **UP / DN**

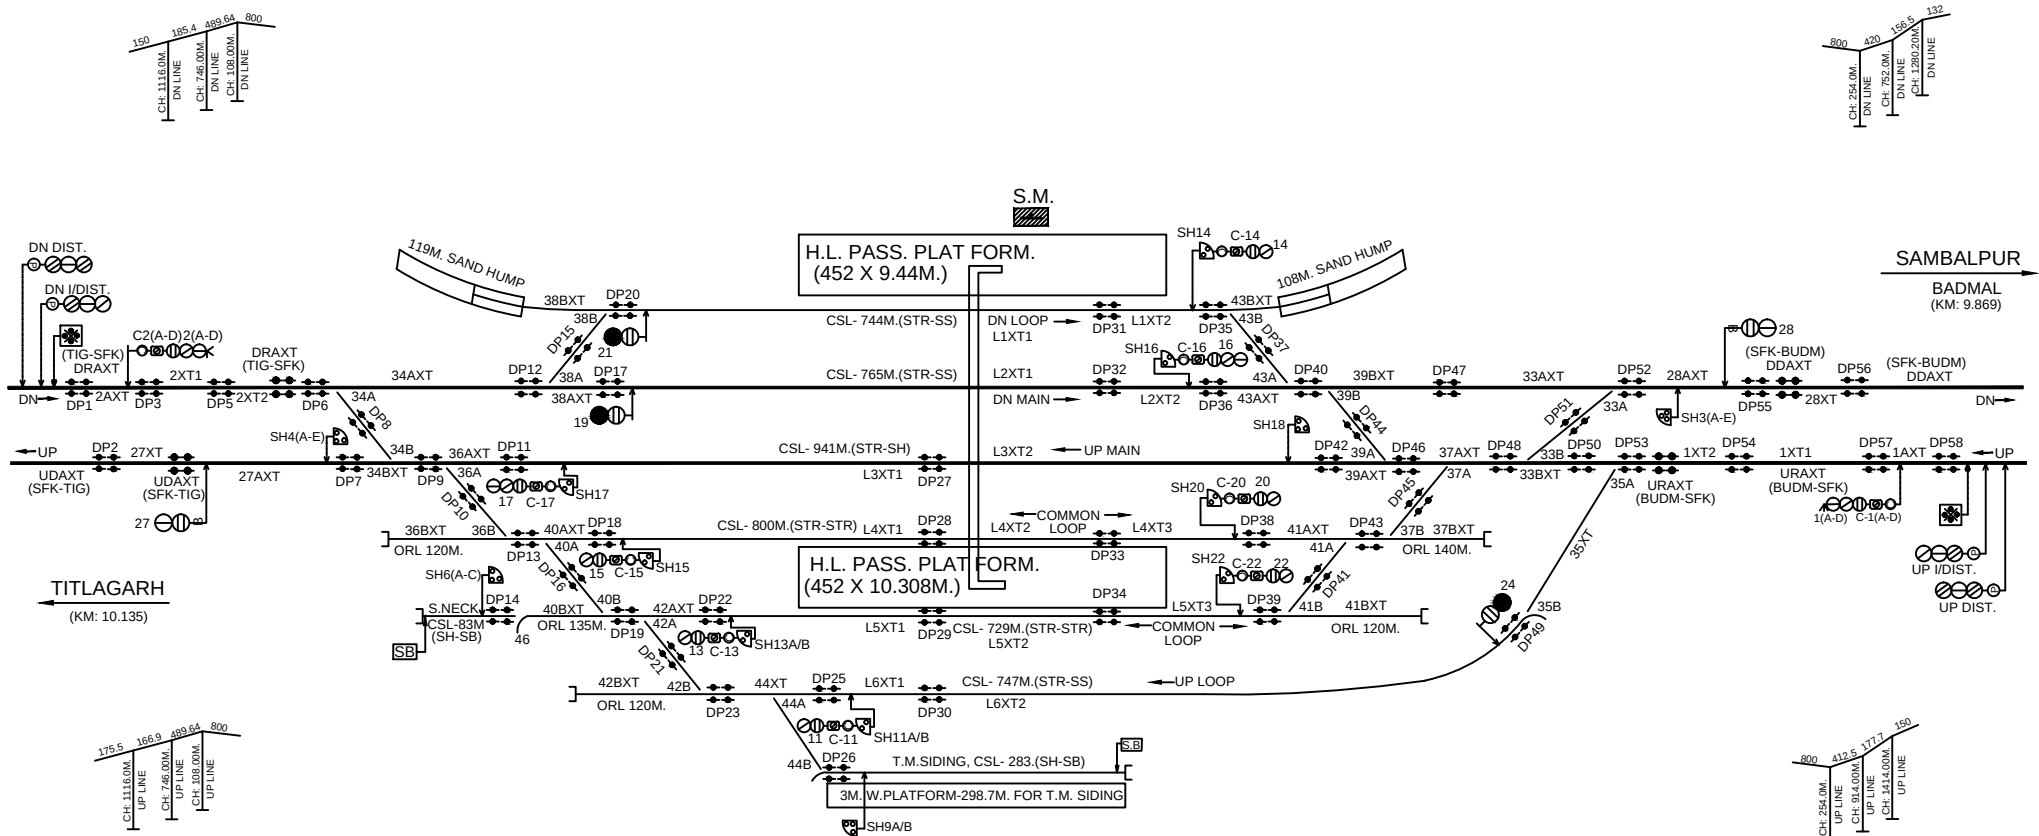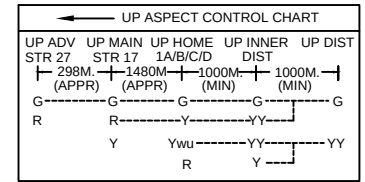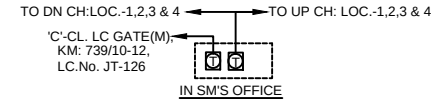

CONTROLS AT S.M. WITH DUAL VDU.

TOTAL NUMBER OF CONTROLS :- 1 TO 50

SIGNAL COTROLS : 1 TO 30.

SPARE : 5.7.8.10.12. 23. 25. 26. 29. 30.

POINTS & OTHER CONTROLS: 31 - 50.

SPARE : 31. 32. 45. 47. 48. 49. 50.


SYSTEM OF WORKING

NO.	SYSTEM	SECTION	INSTRUMENT	LOCATION
1.	ABSOLUTE BLOCK	SIKIR - TITLAGARH	DLBI (SGE)	S.M.
2.	ABSOLUTE BLOCK	SIKIR - BADMAL	DLBI (SGE)	S.M.

CRANK HANDLE GROUPING FOR EMERGENCY OPERATION OF POINTS		
SL. NO.	CRANK HANDLE	CONTROL POINTS
1.	CH1	33A/B, 39A/B.
2.	CH2	36A/B, 37A/B.
3.	CH3	40A/B, 41A/B.
4.	CH4	35A/B.
5.	CH5	38A/B, 43A/B.
6.	CH6	42A/B.
7.	CH7	34A/B.
8.	CH8	44A/B.
9.	CH9	46.

NM: 21.10.22

DN ASPECT CONTROL CHART (SBP END)

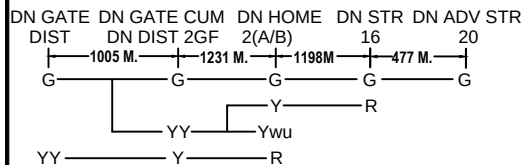


SARLA(SLRA)




I.P.NO.S.I.22069, ALT-'G', (P.I), STD-II(R)
KM: 555.405 F/HWH, KM: 40.800 F/JSG, CL-'B'.

UP / DN

UP ASPECT CONTROL CHART (SBPY END)

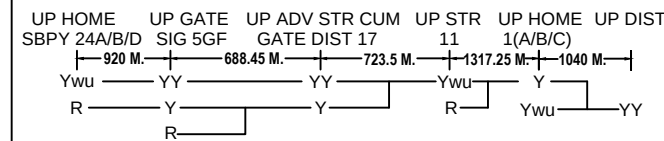

UP ASPECT CONTROL CHART (SBP END)

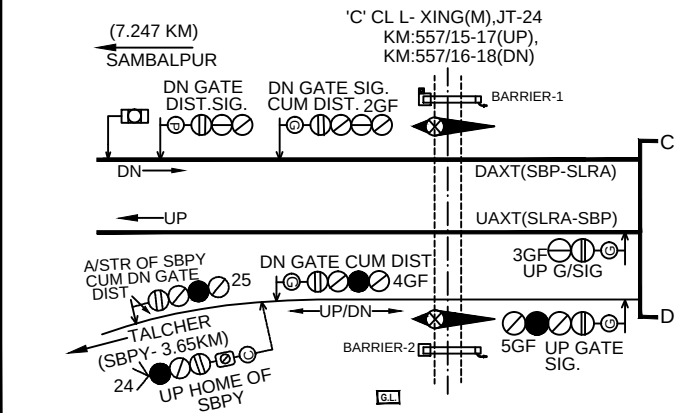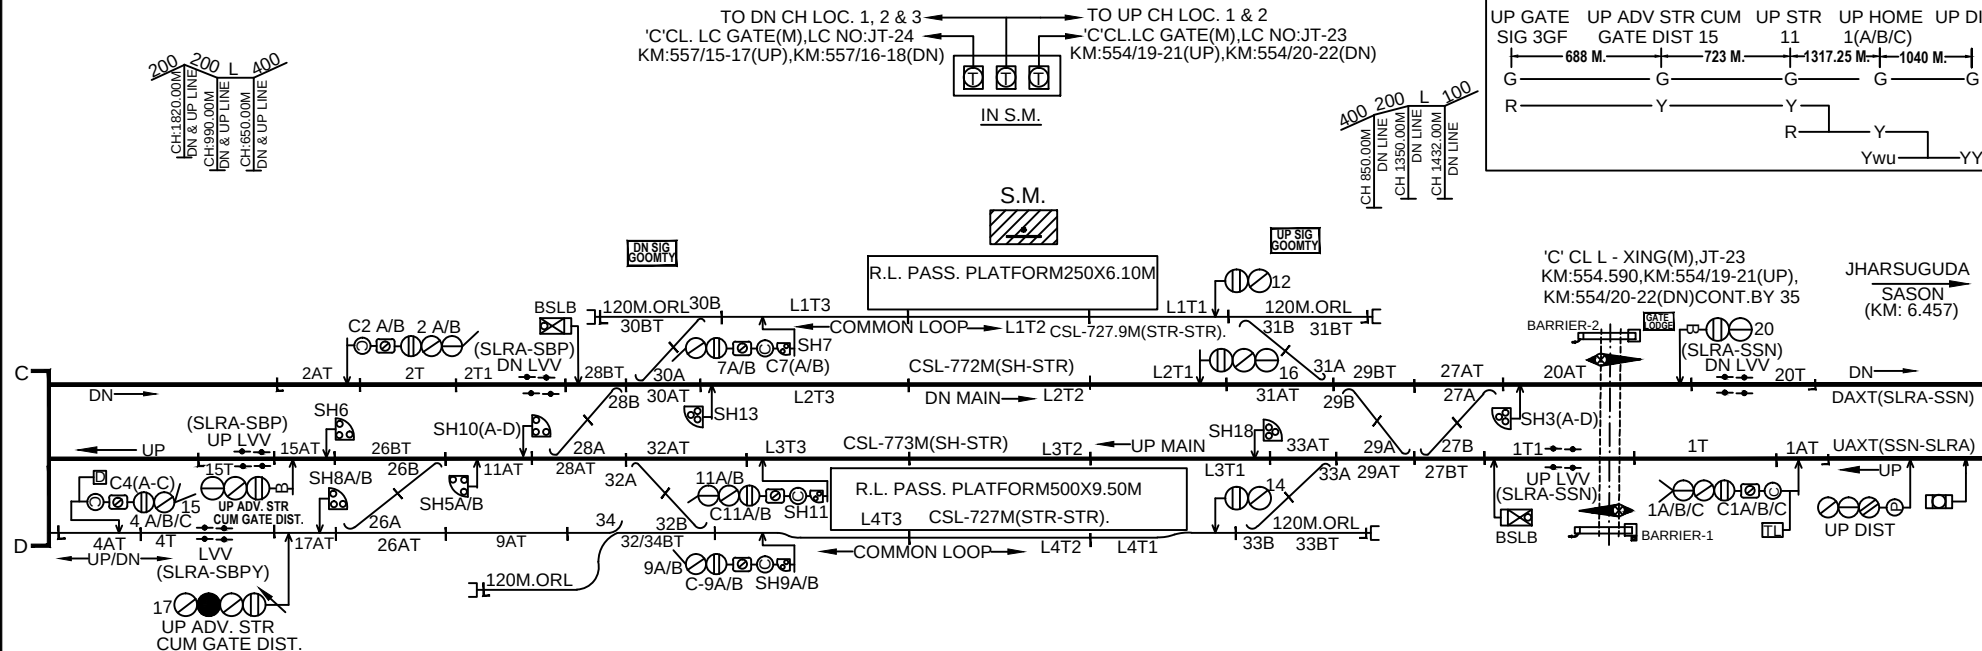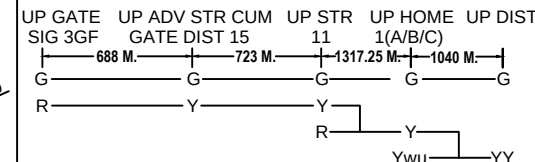

CRANK HANDLE GROUPING FOR EMERGENCY HAND OPERATION OF POINTS

SL. NO.	CRANK HANDLE	CONTROL POINTS
1.	CH1	32.33.
2.	CH2	30.31.
3.	CH3	27.29.
4.	CH4	28.
5.	CH3	26.
6.	CH4	34.

CONTROL PANEL IN S.M.

TOTAL NUMBER OF CONTROLS :- 1 TO 50


SIGNAL CONTROL :- 1 TO 18 & 20

POINTS & OTHER CONTROL :- 26 TO 35

SPARE :- 19,21,22,23,24,25 & 36 TO 50

SYSTEM OF WORKING








No.	SYSTEM	SECTION	INSTRUMENT	LOCATION
1.	ABSOLUTE BLOCK	SLRA-SBP	DLBI	SM's ROOM
2.	ABSOLUTE BLOCK	SLRA-SBPY	TLBI(FM DIADO)	SM's ROOM
3.	ABSOLUTE BLOCK	SLRA-SSN	DLBI	SM's ROOM

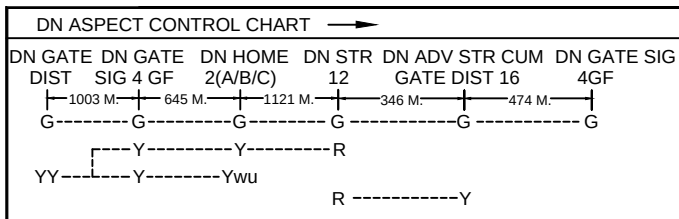



SASON(SSN)

S.I. NO. 22086 ALT-'F', (P.I)
KM:- 548.948 F/HWH,STD-II(R)
KM:- 34.343 F/JSG, CL-'B'.

UP / DN

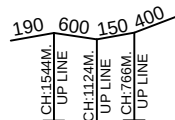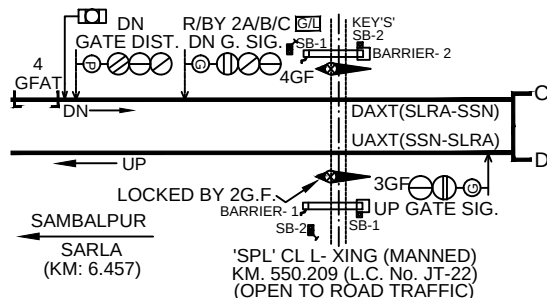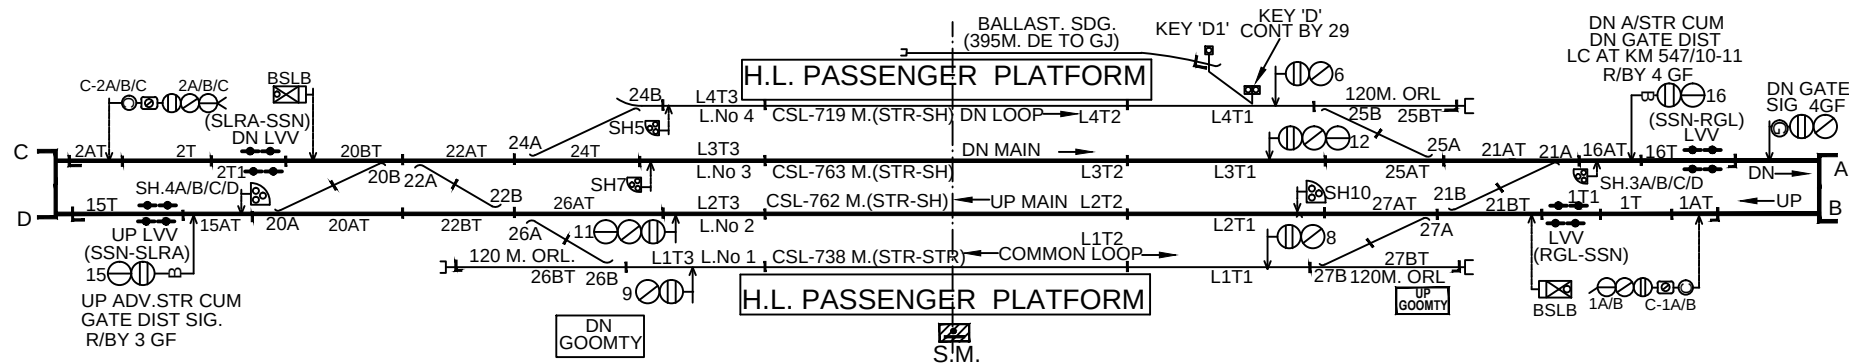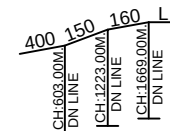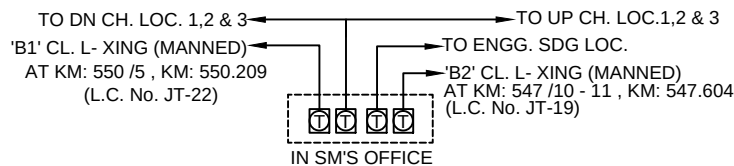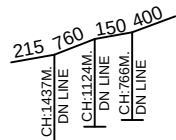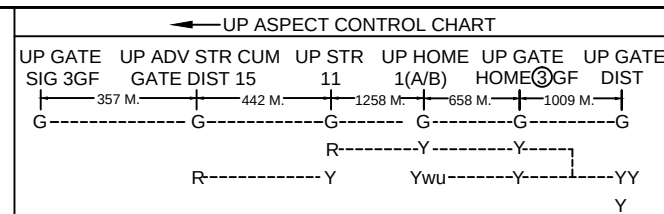

'A' CL L- XING (M),LC NO:-JT-19,
KM:547/27-29(UP),KM:547/28-30(DN)
(OPEN TO ROAD TRAFFIC)

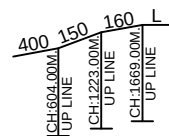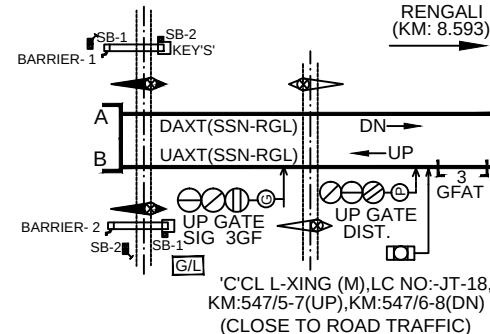

SYSTEM OF WORKING				
No.	SYSTEM	SECTION	INSTRUMENT	LOCATION
1.	ABSOLUTE BLOCK	SASON-SARLA	DLBI	SM's ROOM
2.	ABSOLUTE BLOCK	SASON-RENGALI	DLBI	SM's ROOM

CRANK HANDLE GROUPING FOR EMERGENCY OPERATION OF POINTS		
SL. NO.	CRANK HANDLE	CONTROL POINTS
1.	CH1	26.27.
2.	CH2	24.25.
3.	CH3	20.22.
4.	CH4	21.


CONTROL PANEL IN S.M.

TOTAL NUMBER OF CONTROLS :- 1 TO 50



SIGNAL CONTROLS :- 1 TO 12, 15 & 16

POINTS & OTHER CONTROLS :- 20,21,22,24-27,29

SPARE :- 13,14,17,18,19,23,28 & 30 TO 50

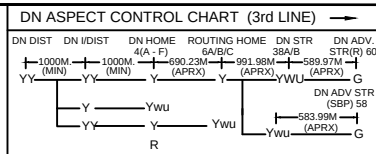

S.I. NO. - 22216, ALT-'A', (E.I.)
KM:- 202.686 FROM RAIPUR,
STD - III(R), CL- 'B'.

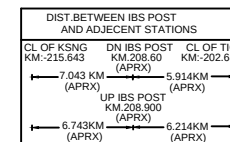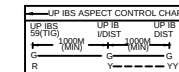

CRANK HANDLE CONTROL FOR EMERGENCY OPERATION OF POINTS		
NO.	CRANK HANDLE	CONTROL POINTS
1.	CH5	102A/B, 111A/B
2.	CH2	113A/B
3.	CH3	103A/B, 109A/B
4.	CH4	105A/B, 107A/B
5.	CH6	110A/B, 117, 119A/B
6.	CH8	121, 123A/B, 125
7.	CH7	127A/B
8.	CH9	129, 131A/B
9.	CH10A/B	108A/B, 112A/B
10.	CH10	110A/B, 104A/B
11.	CH11	128A/B, 132A/B
12.	CH12	130
13.	CH13	134, 136, 138A/B
14.	CH14	140, 142A/B
15.	CH15	106A/B, 114, 116, 118A/B
16.	CH16	120, 126A/B, 126

