



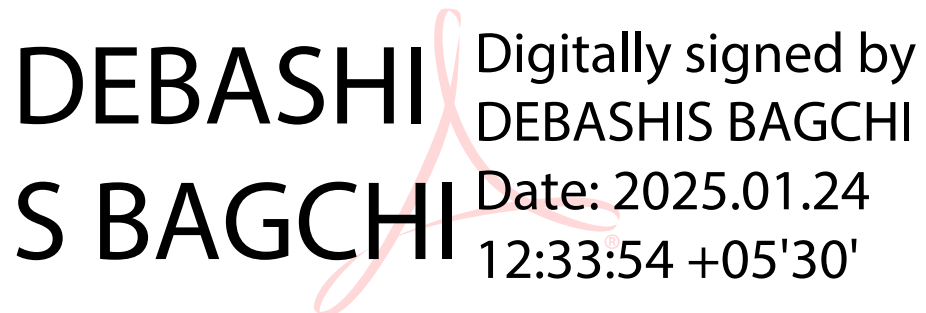



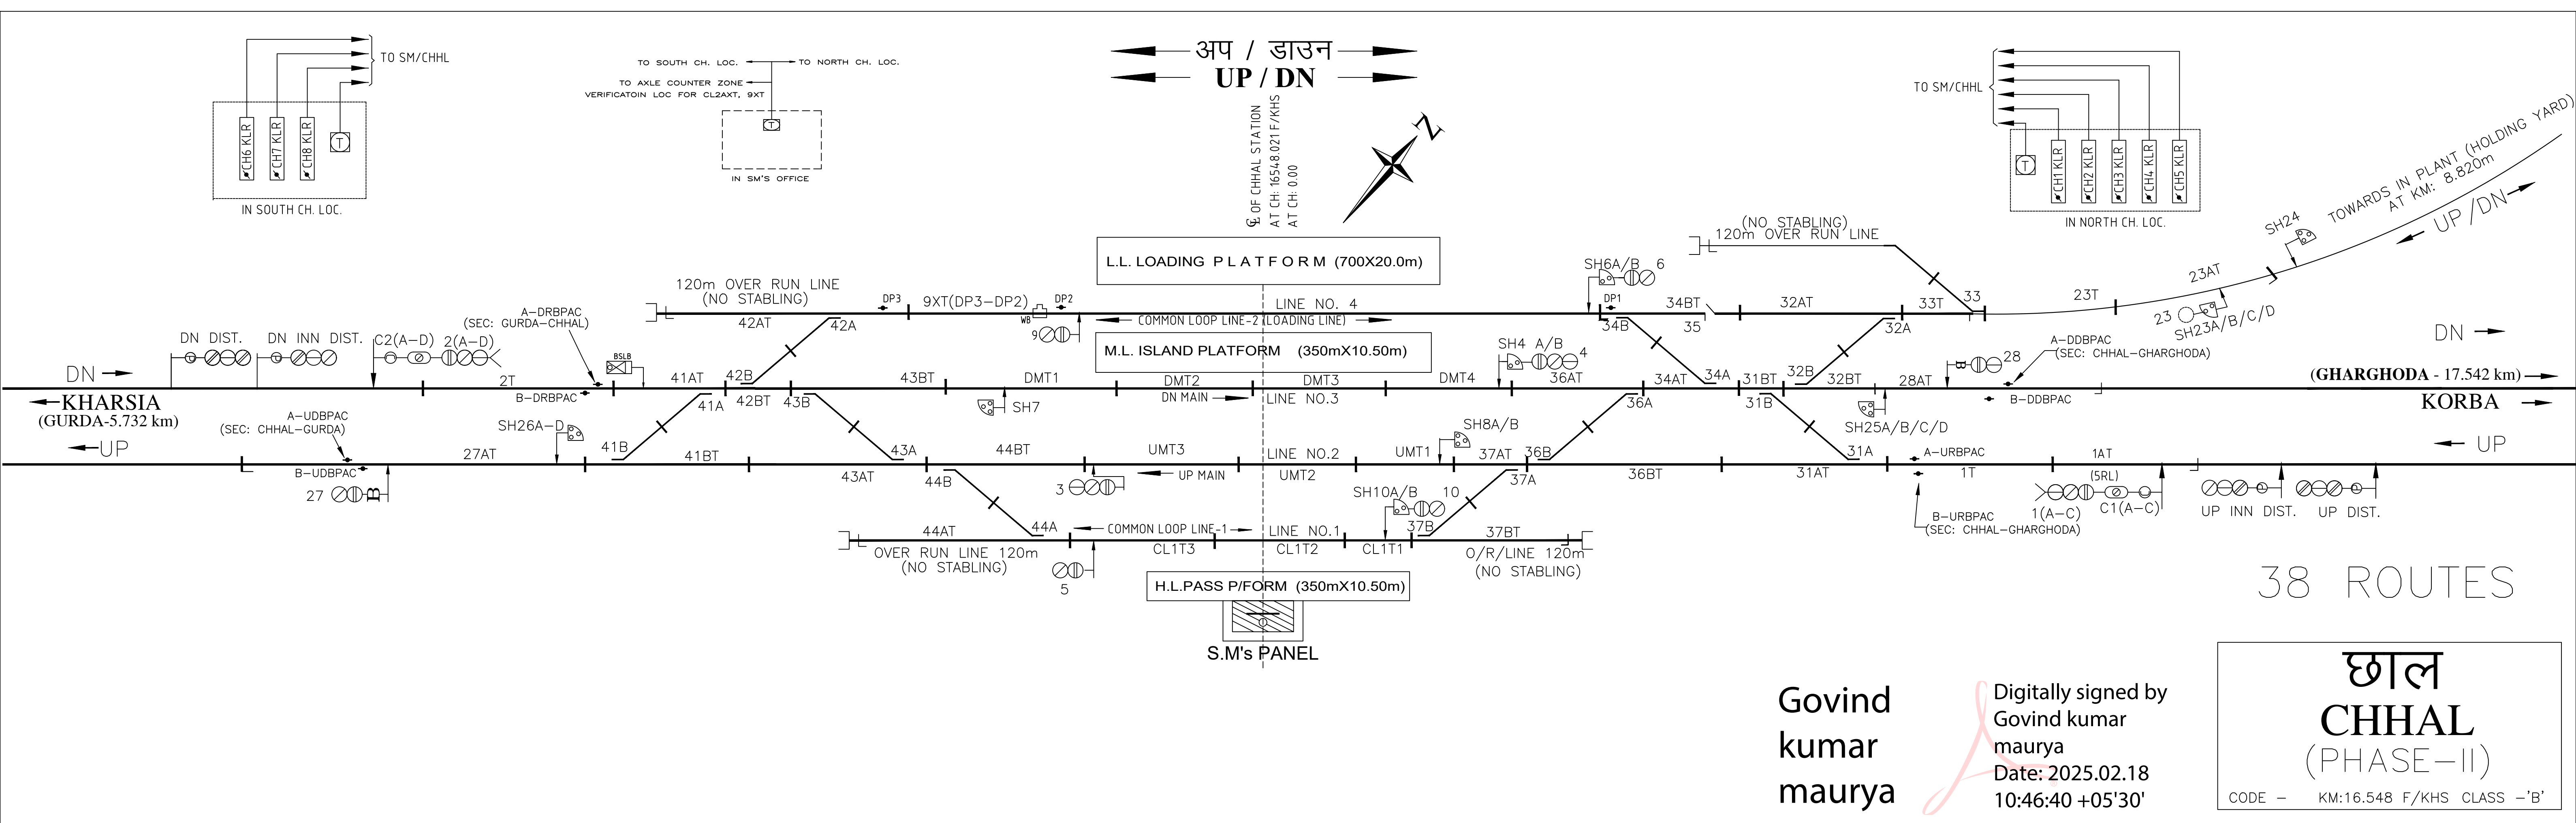



धरमजयगढ़ रोड

DHARAMJAIGARH ROAD

(PHASE-I)

CLASS 'B'

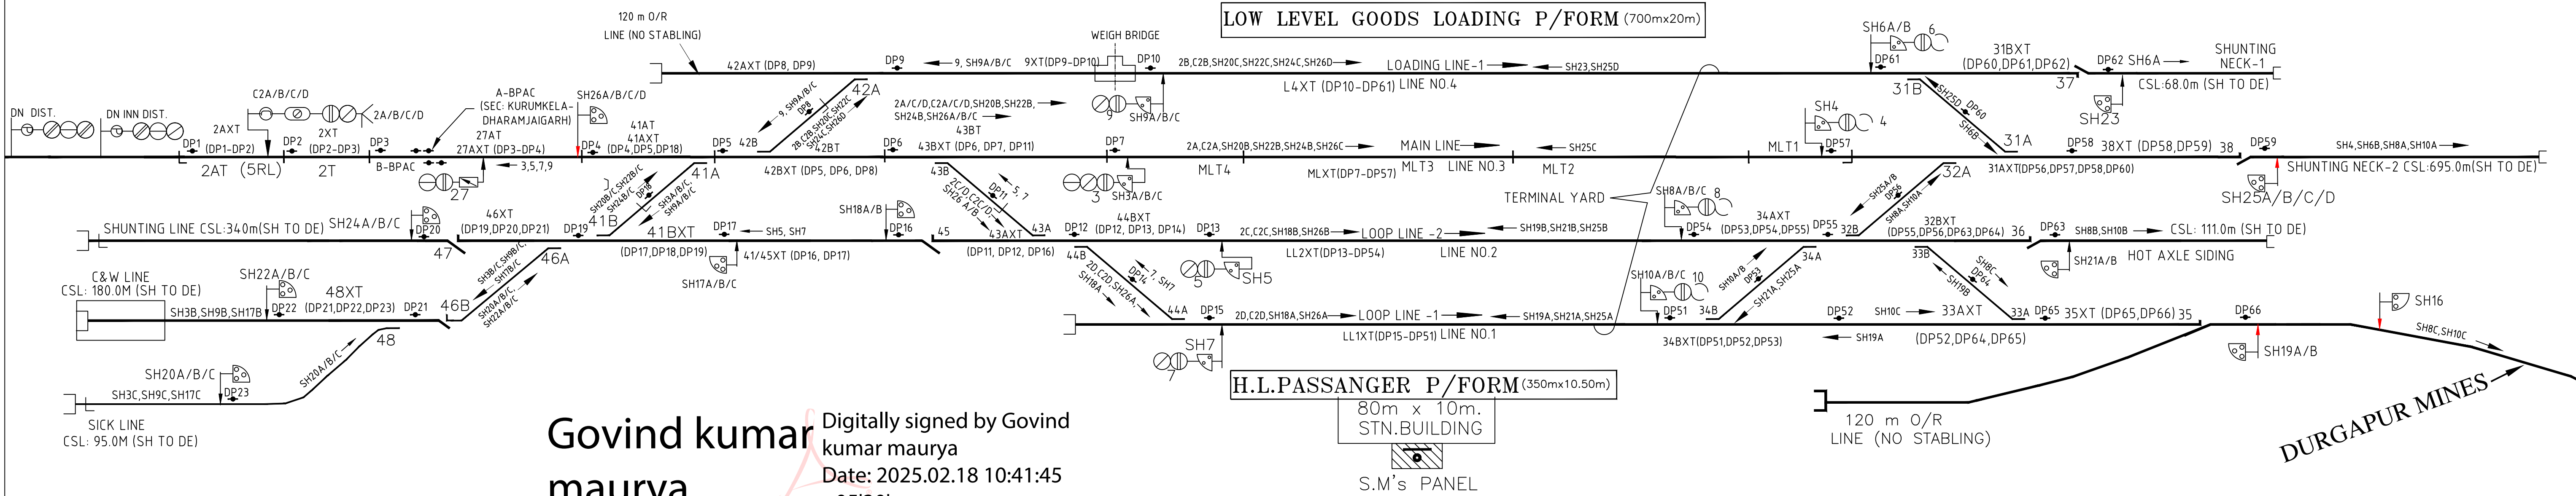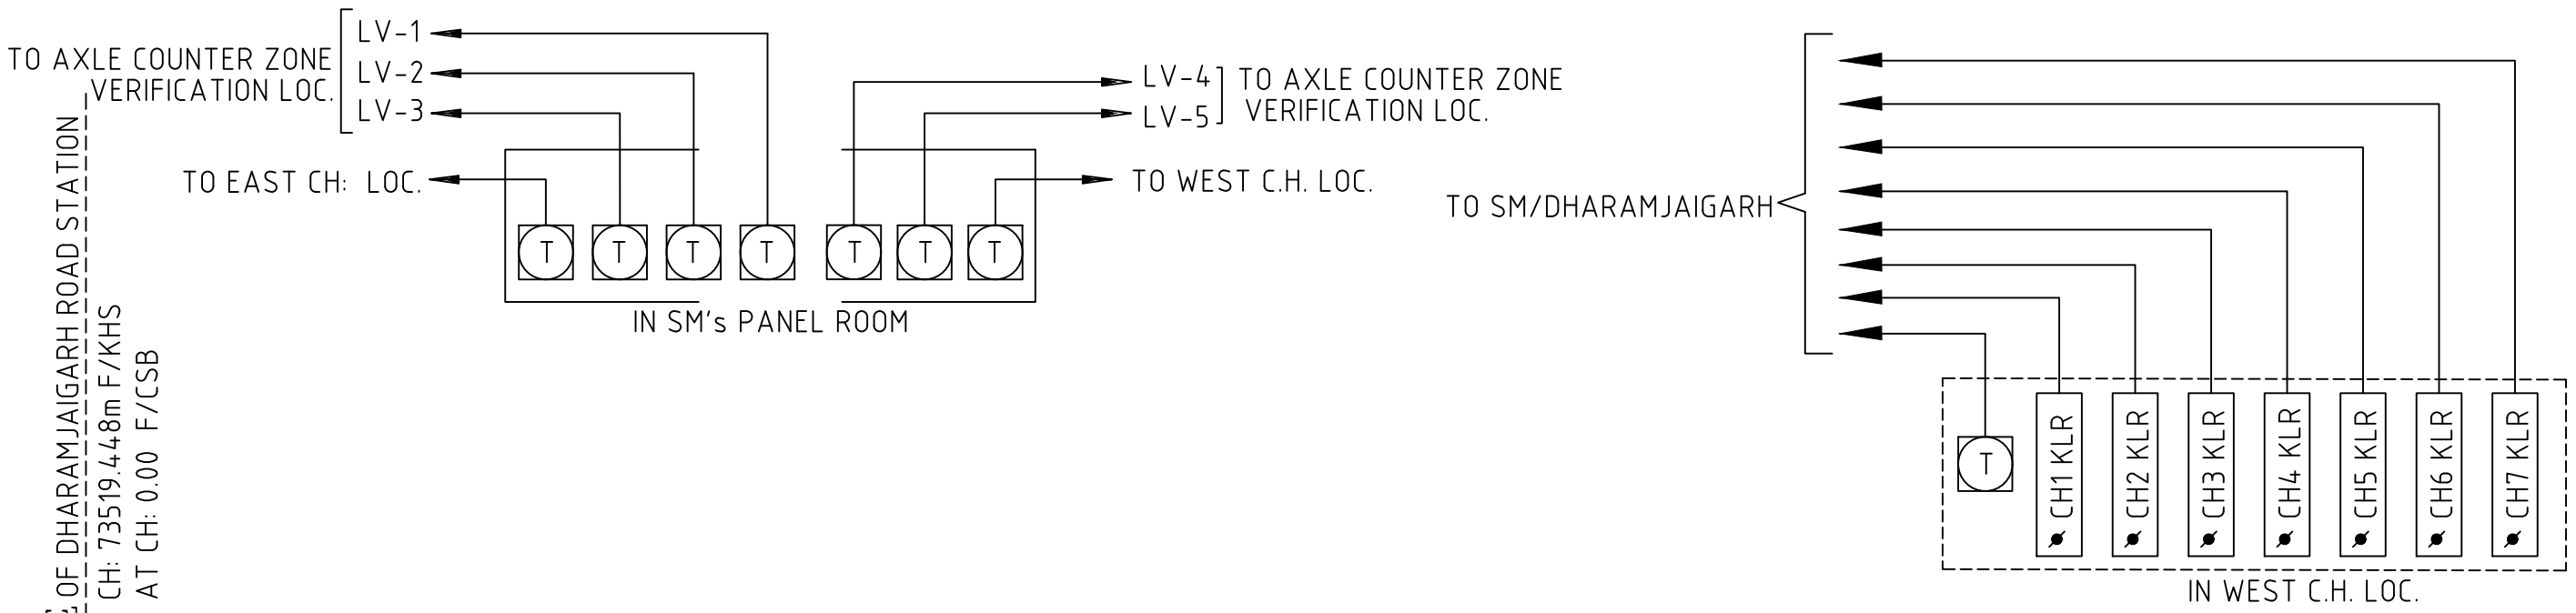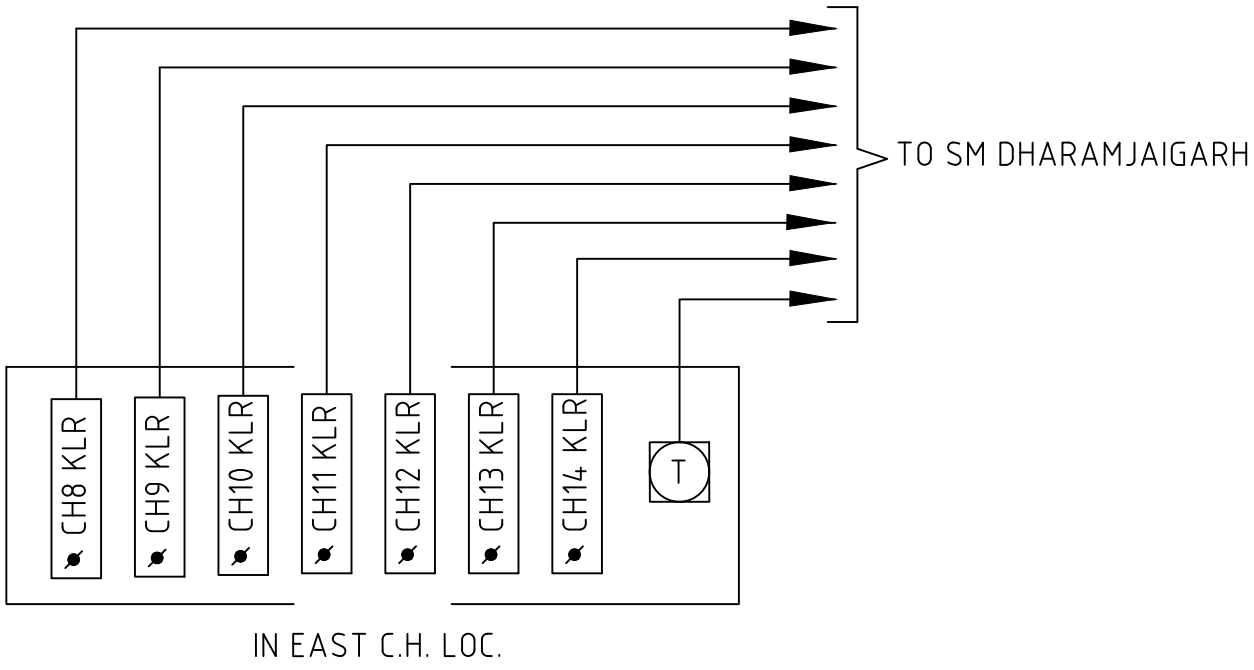


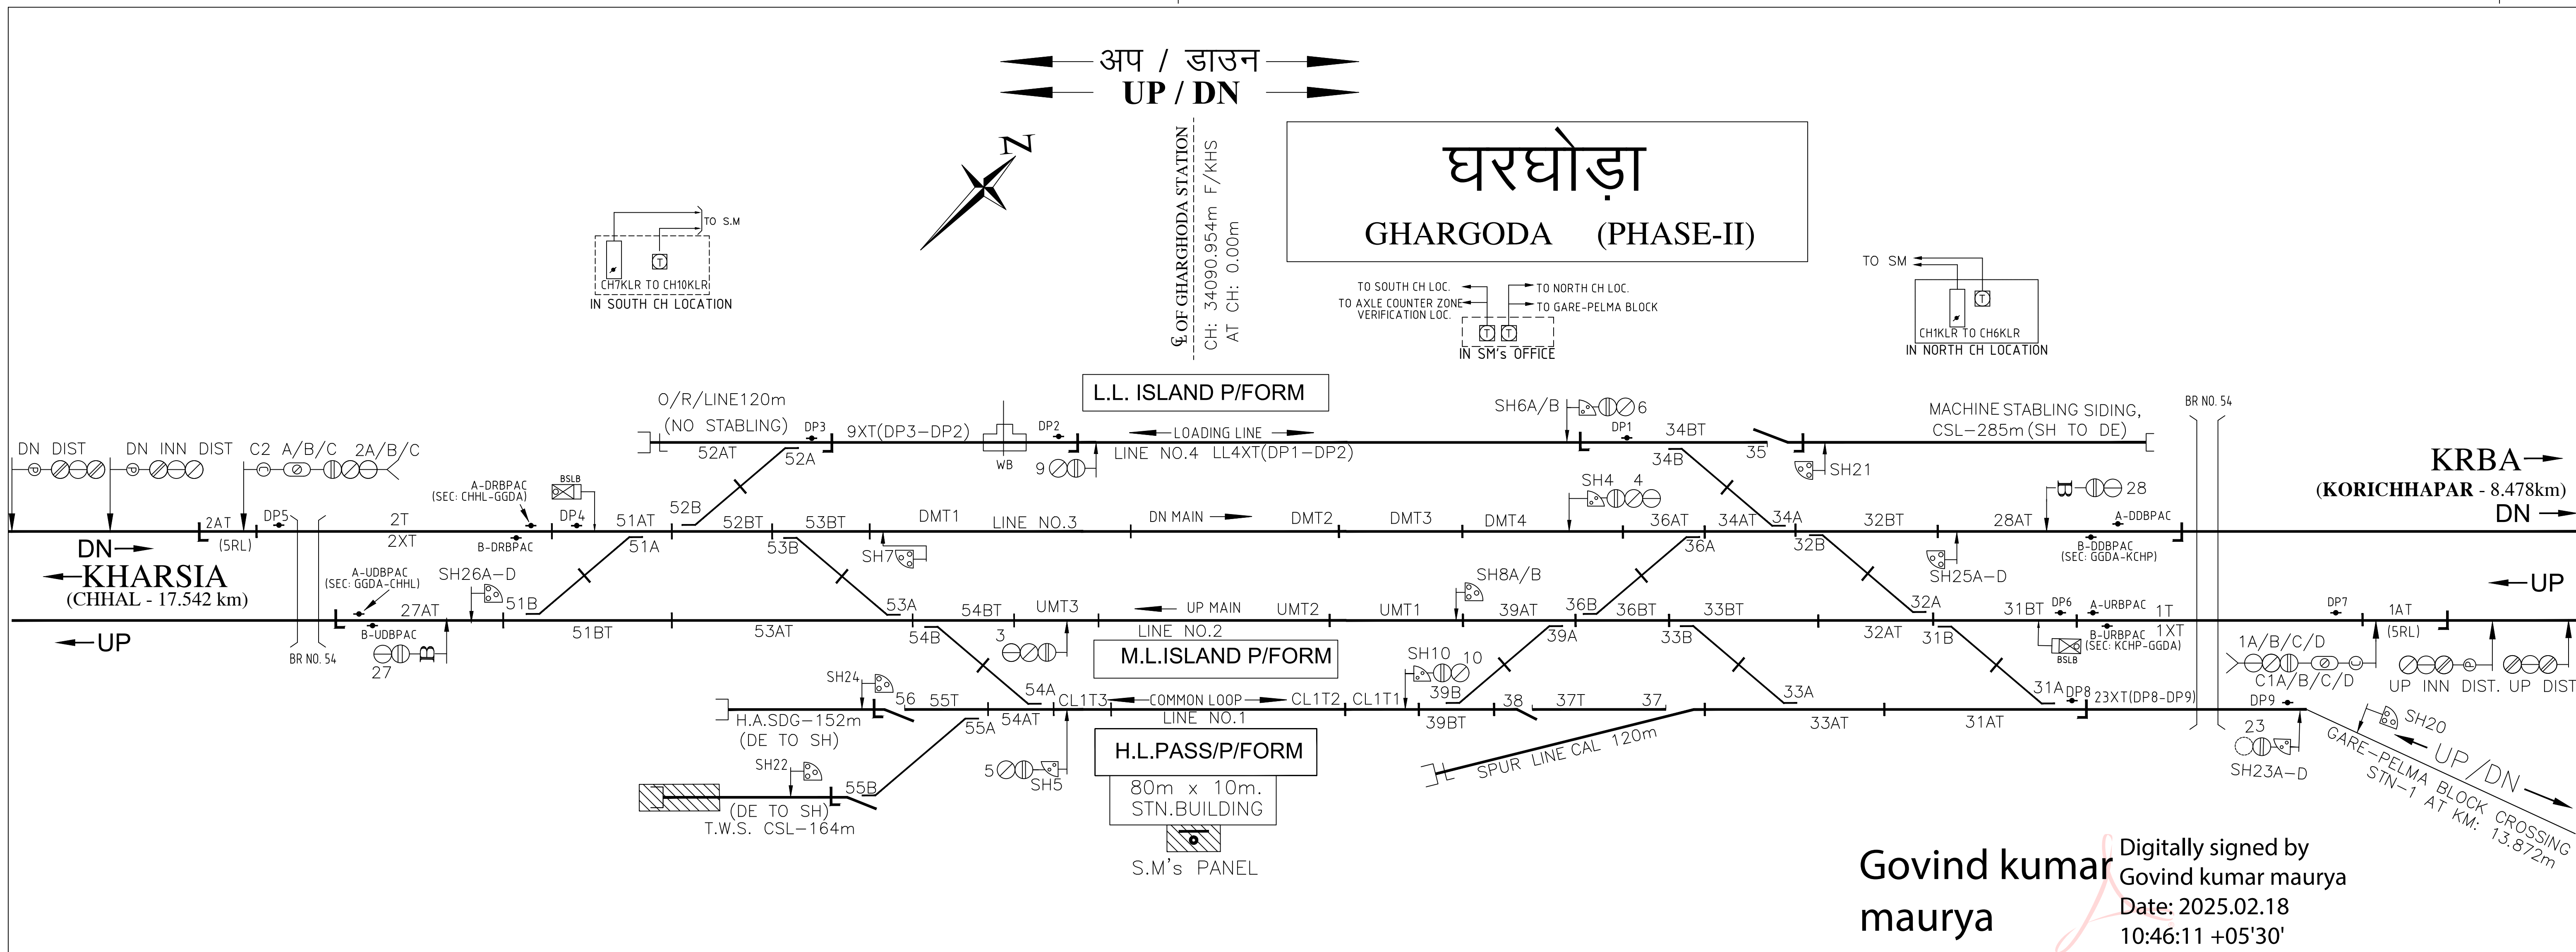

KM 10.815 F/KHS CLASS 'B'





 अप / डाउन
 UP / DN

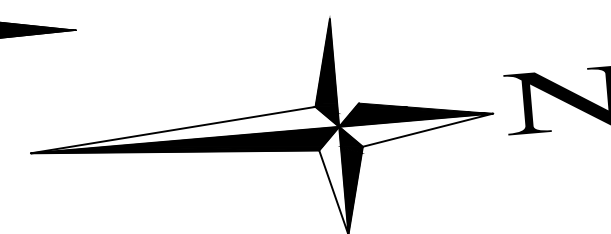

TO SOUTH CH LOC. ←

→ TO NORTH CH LOC.

IN SM'S OFFICE

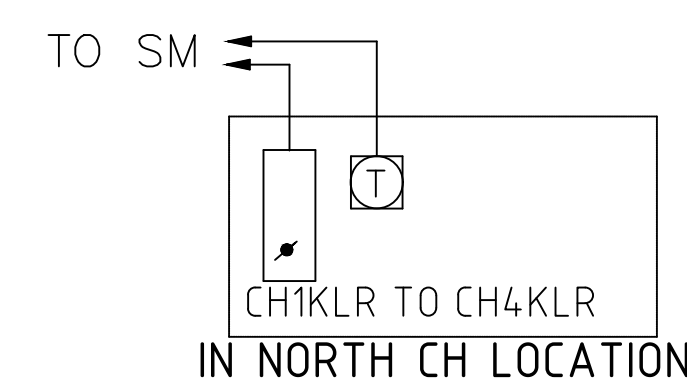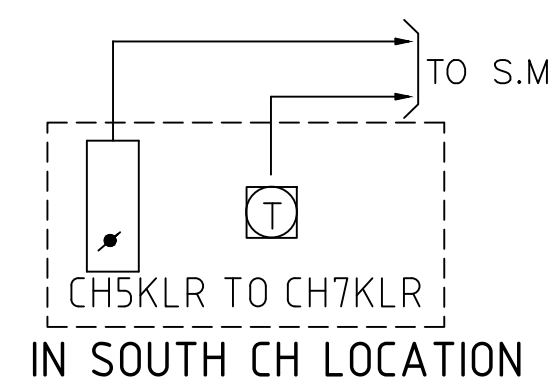


1
 2 £ OF GURDA STATION
 3 CH: km: 10.815 F/K
 4 AT CH: 0.00

S.M's PANEL

STN.BUILDING
80m x 10m.


H.L.PASS. P/FORM
(350m x10.5m)

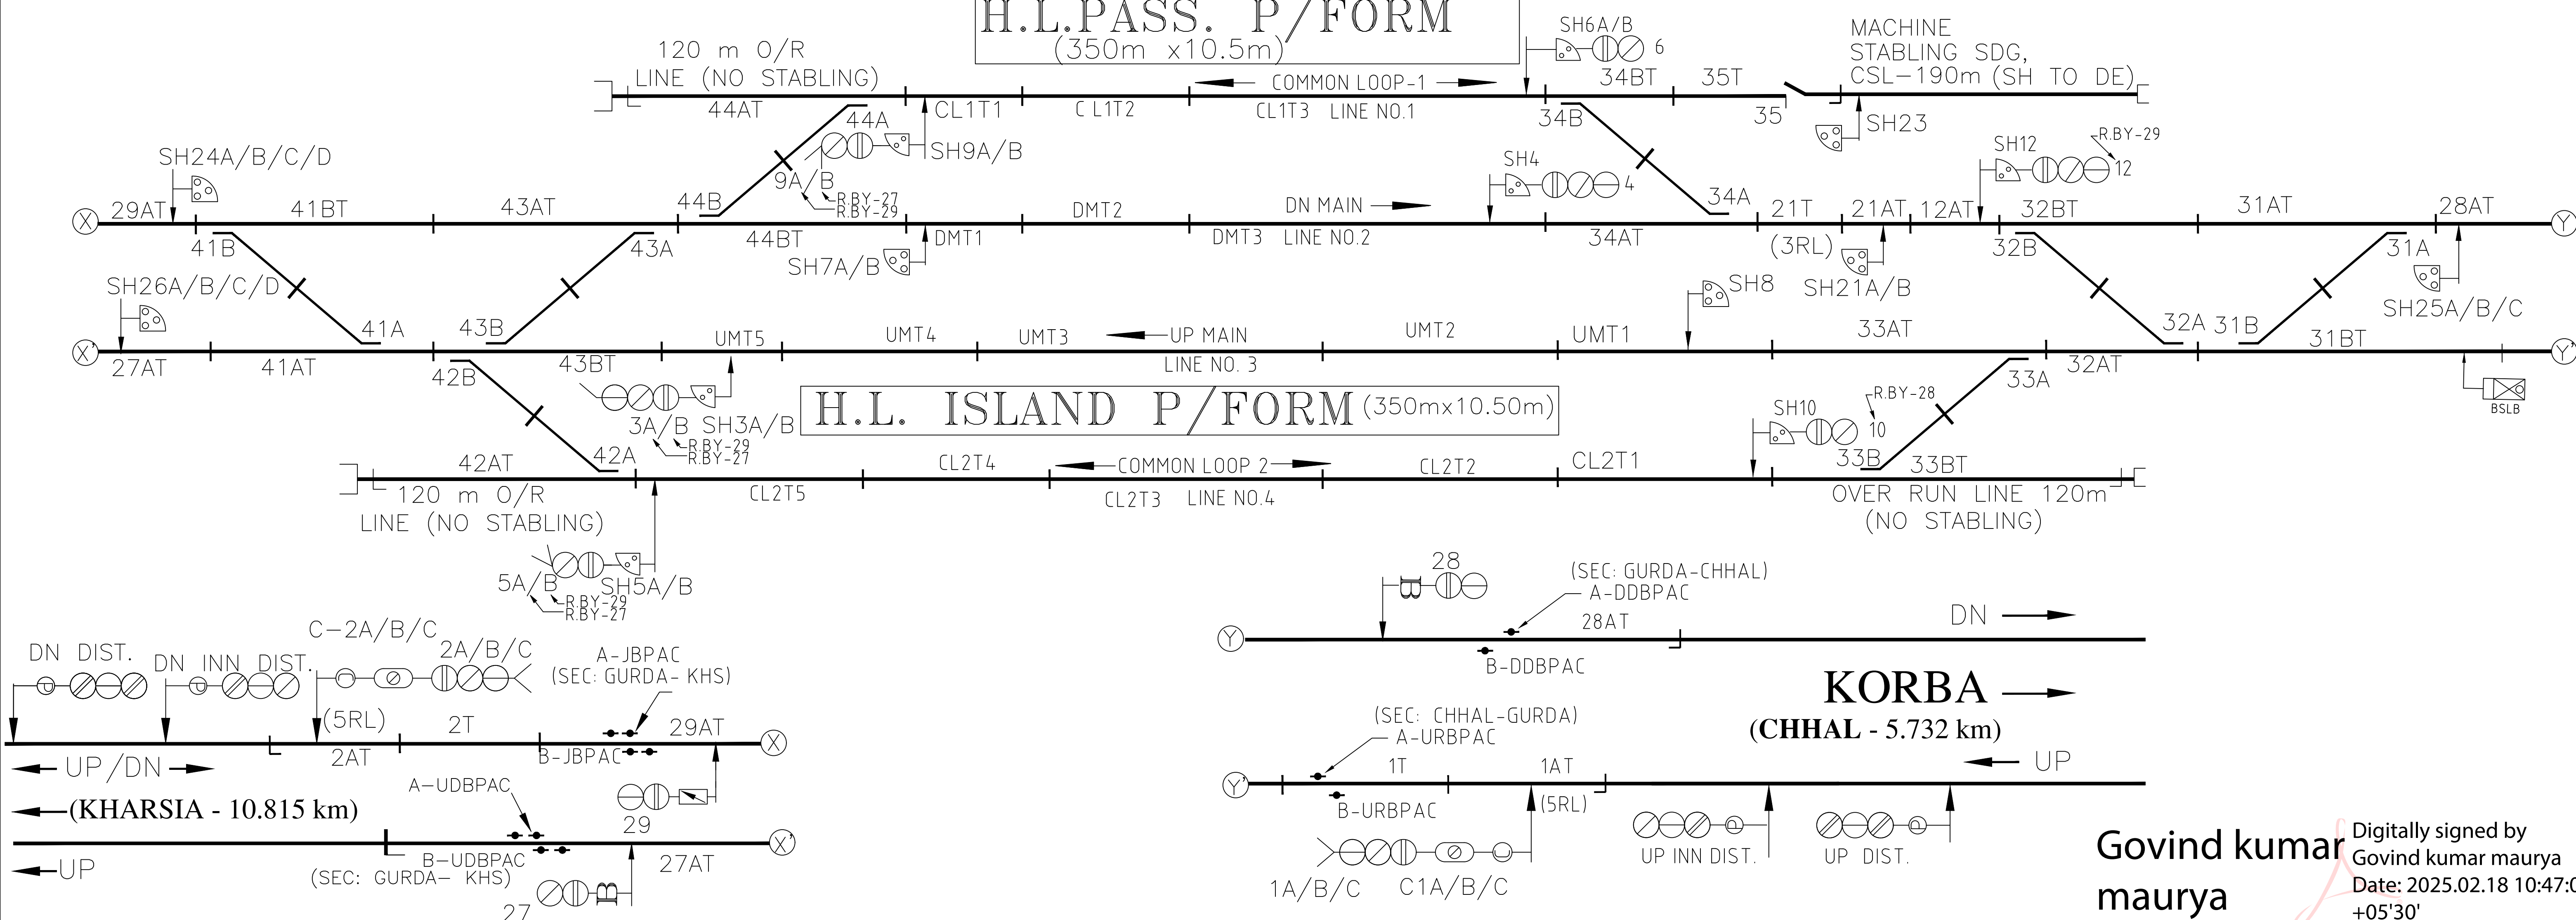

Govind kumar
maurya

Digitally signed by
Govind kumar maurya
Date: 2025.02.18 10:47:06
+05'30'

कोरीछापर
KORICHHAPAR(PHASE-II)

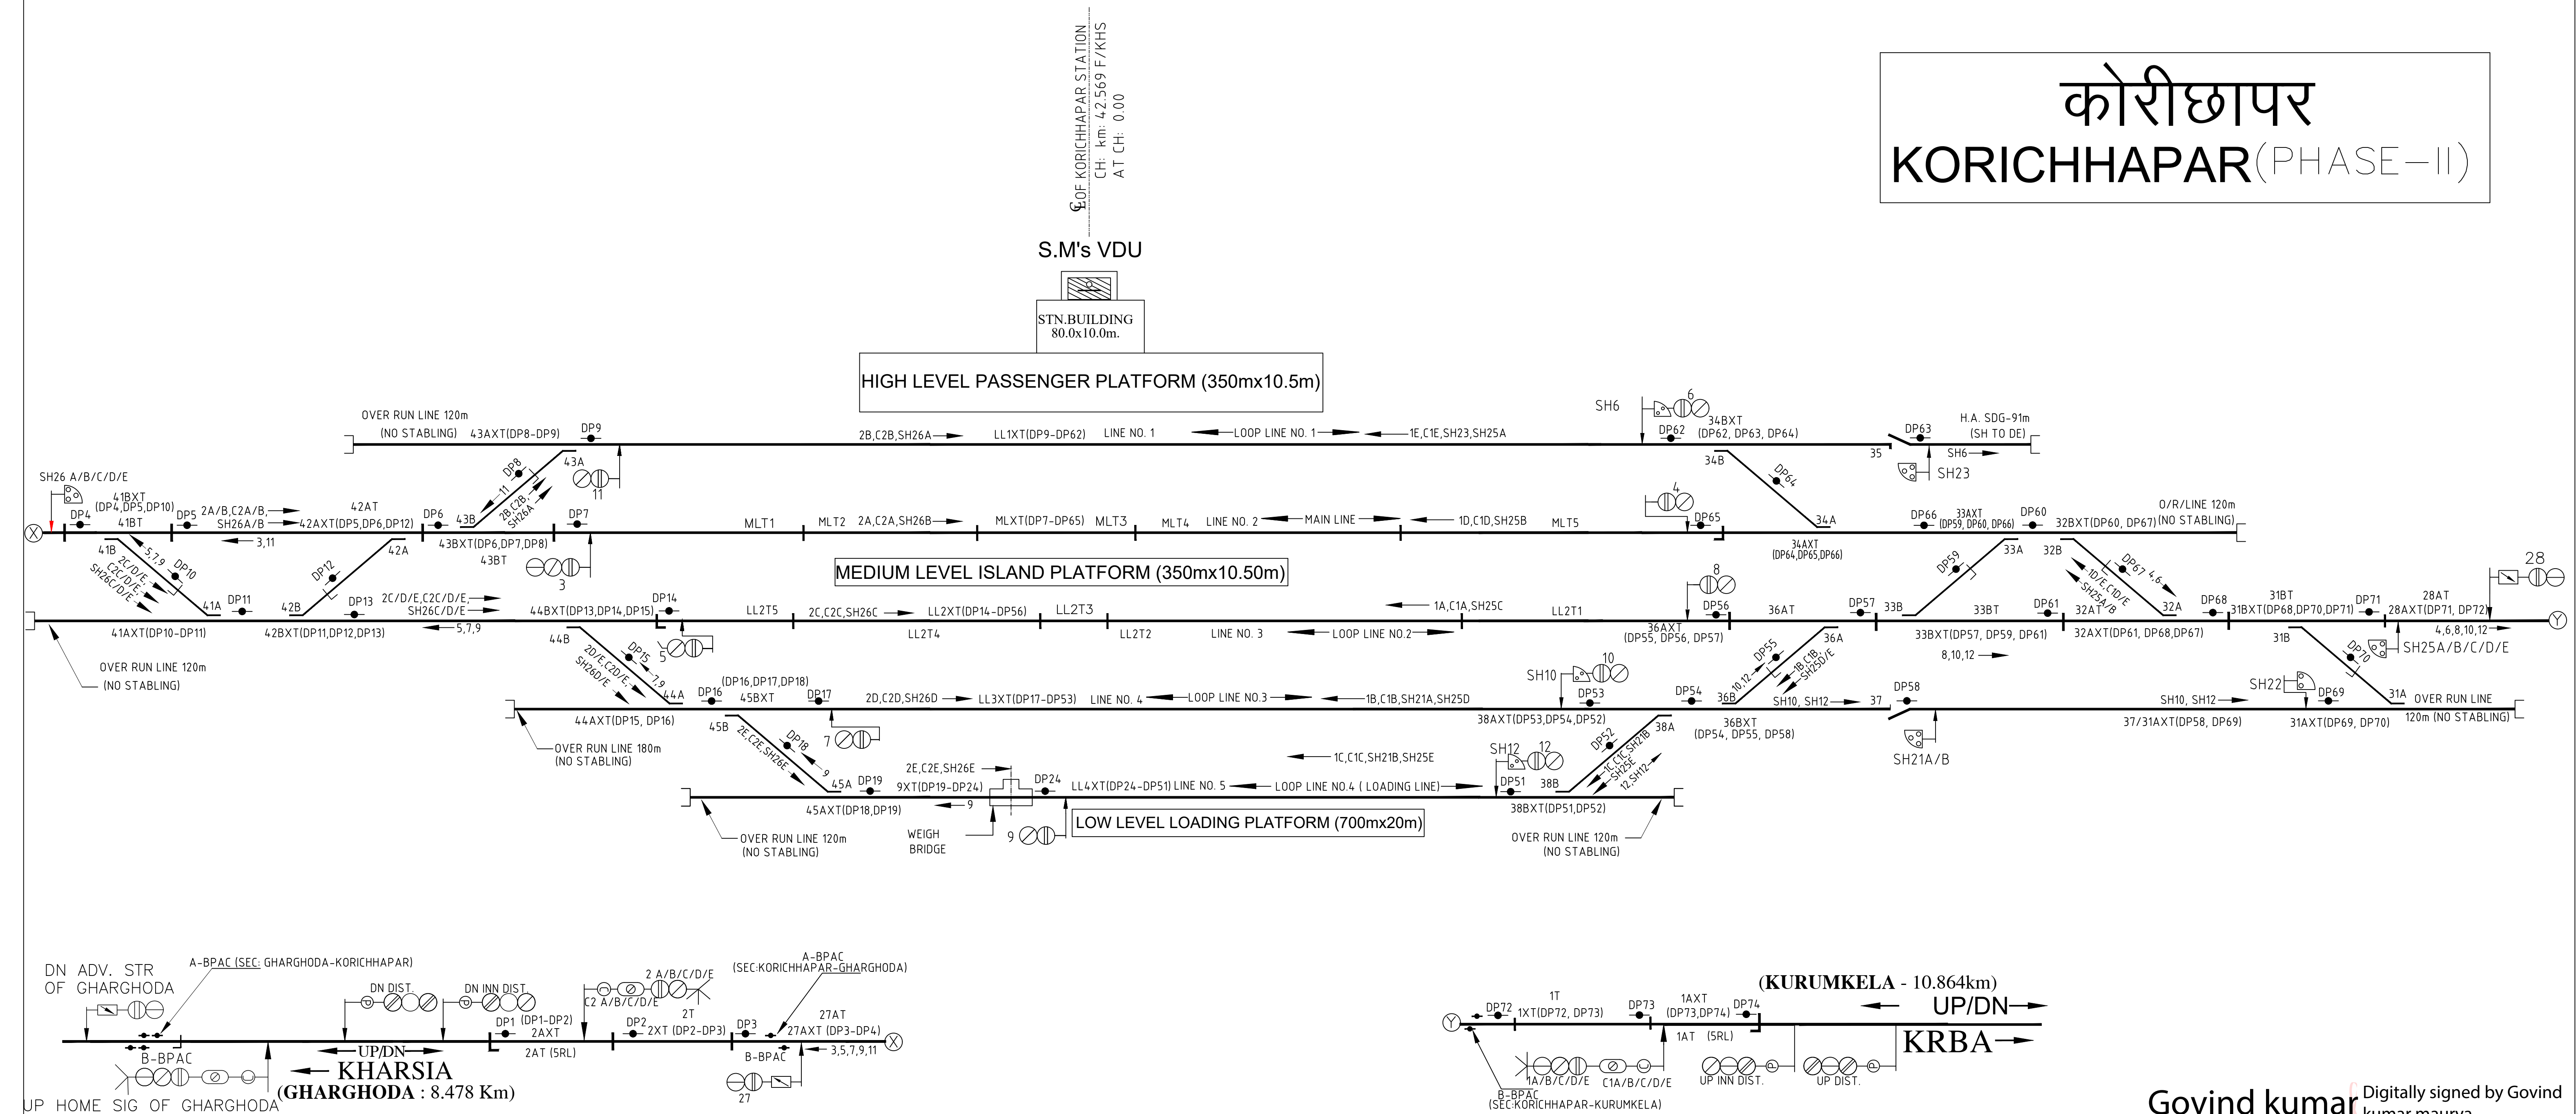

Govind kumar
maurya


Digitally signed by Govind
kumar maurya
Date: 2025.02.18 10:45:36
+05'30'

कुरुमकेला

KURUMKELA

(PHASE-I)

Km: 53.434007m F/GHARGHODA CLASS 'B'

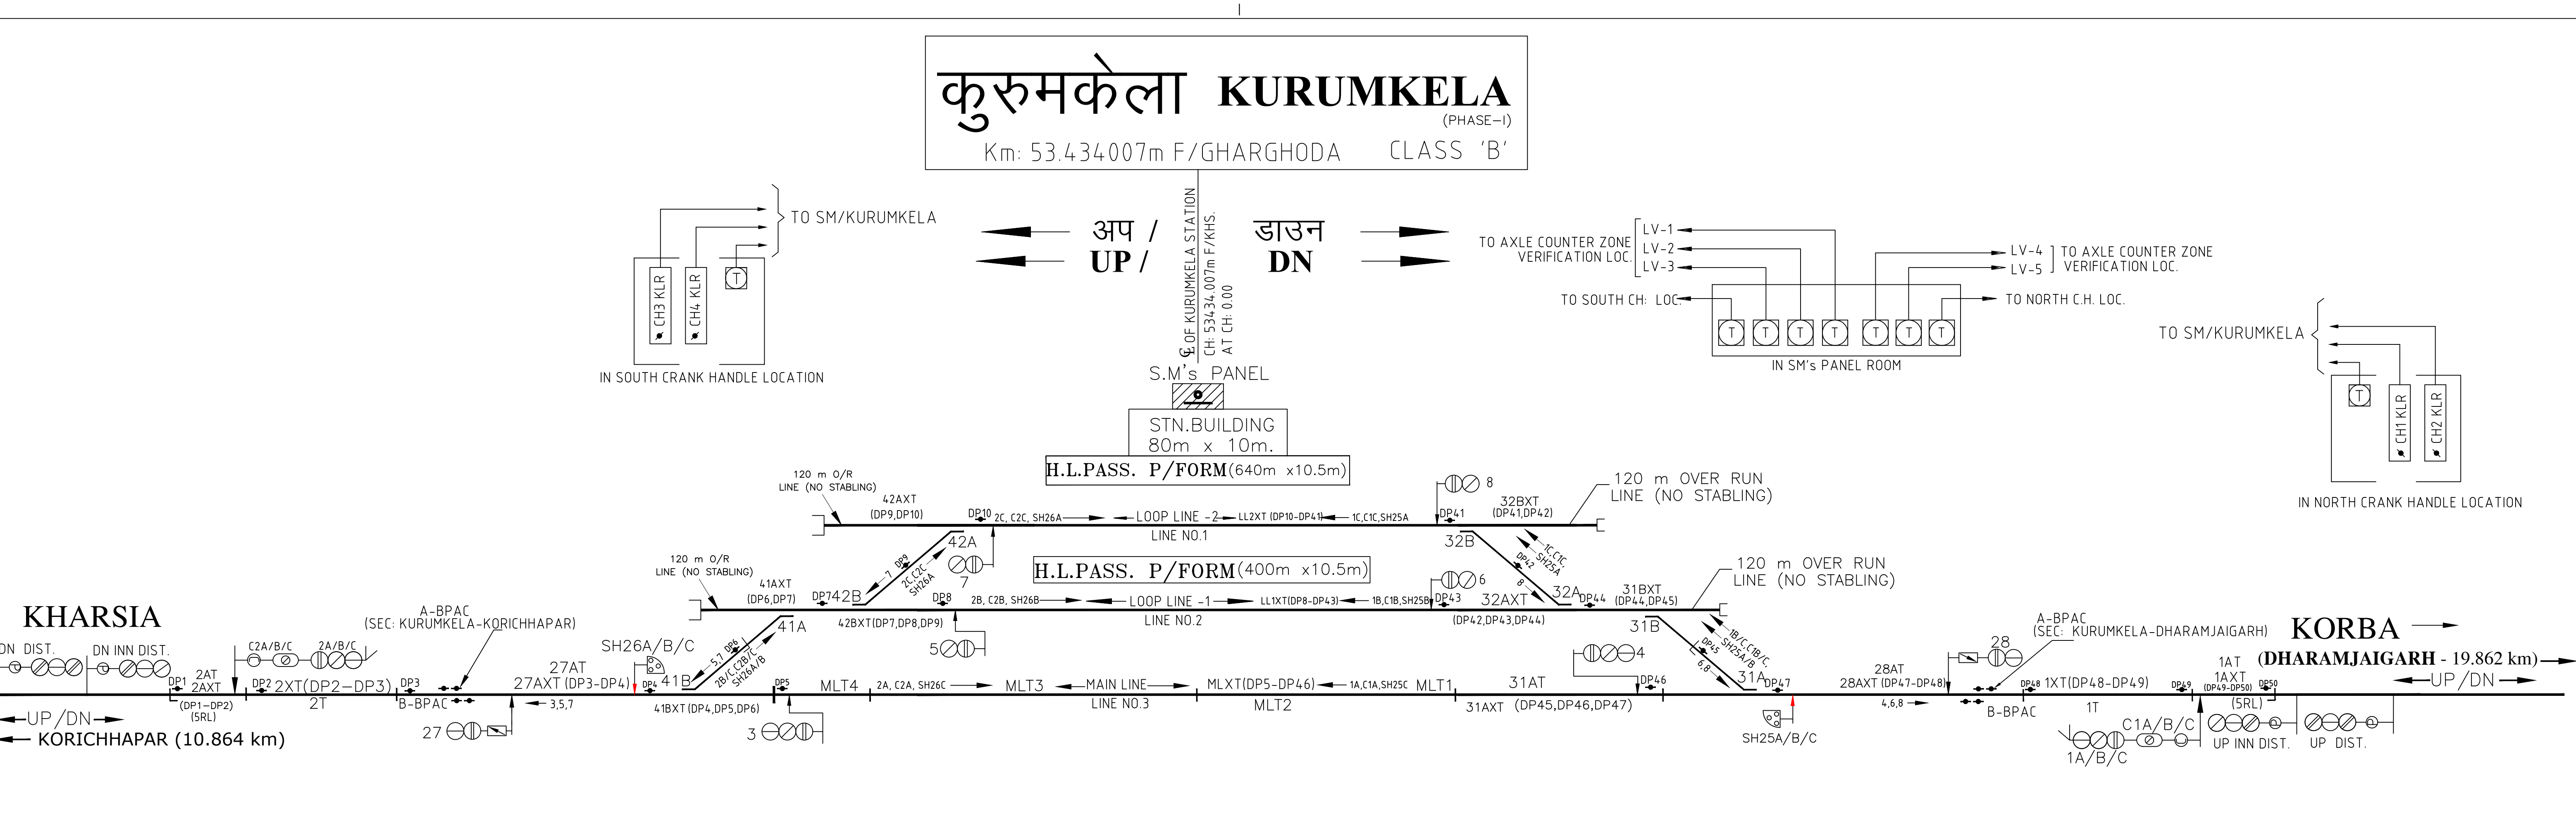

Govind kumar

maurya

Digitally signed by

Govind kumar maurya

Date: 2025.02.18 10:45:12

+05'30'